

Zeszyt projektowy

Zawartość opracowania:

I Opracowanie rysunkowe:

Rys. 1. Inwentaryzacja, skala 1:50

Rys. 2. Zmiany budowlane i wytyczne do hydrauliki, skala 1:50

Rys. 3. Podział na strefy funkcjonalne, skala 1:50

Rys. 4. Układ funkcjonalny, skala 1:50

Rys. 5. Wytyczne do oświetlenia, skala 1:50

Rys. 6. Wytyczne do elektryki, skala 1:50

Rys. 7. Aranżacja podłóg, skala 1:50

Rys. 8. Gładzie i malowanie ścian, skala 1:50

Rys. 9. Przekroje A-A, B-B, C-C, D-D, skala 1:50

Rys. 10. Widoki A-A, B-B, C-C, D-D, skala 1:50

Rys. 11. Rzut części barowej, skala 1:25

Rys. 12. Składowanie części barowej, skala 1:25

Rys. 13. Składowanie zmywalni, skala 1:25

Rys. 14. Składowanie pomieszczenia socjalnego, skala 1:25

Rys. 15. Składowanie pomieszczenia gospodarczego, skala 1:25

Rys. 16. Pergola – przekrój z detalem, skala 1:50

Rys. 17. Pergola - widoki E-E, F-F, skala 1:50

II Opracowanie kolorystyczne


Rys. 18. Rzut kolorystyczny – aranżacja wnętrza, skala 1:50

Rys. 19. Widoki kolorystyczne A-A, B-B, C-C, D-D, skala 1:50

Rys. 20. Widok kolorystyczny baru, skala 1:25




Rys. 21. Pergola – widoki kolorystyczne E-E, F-F, skala 1:50



III Specyfikacja wyposażenia






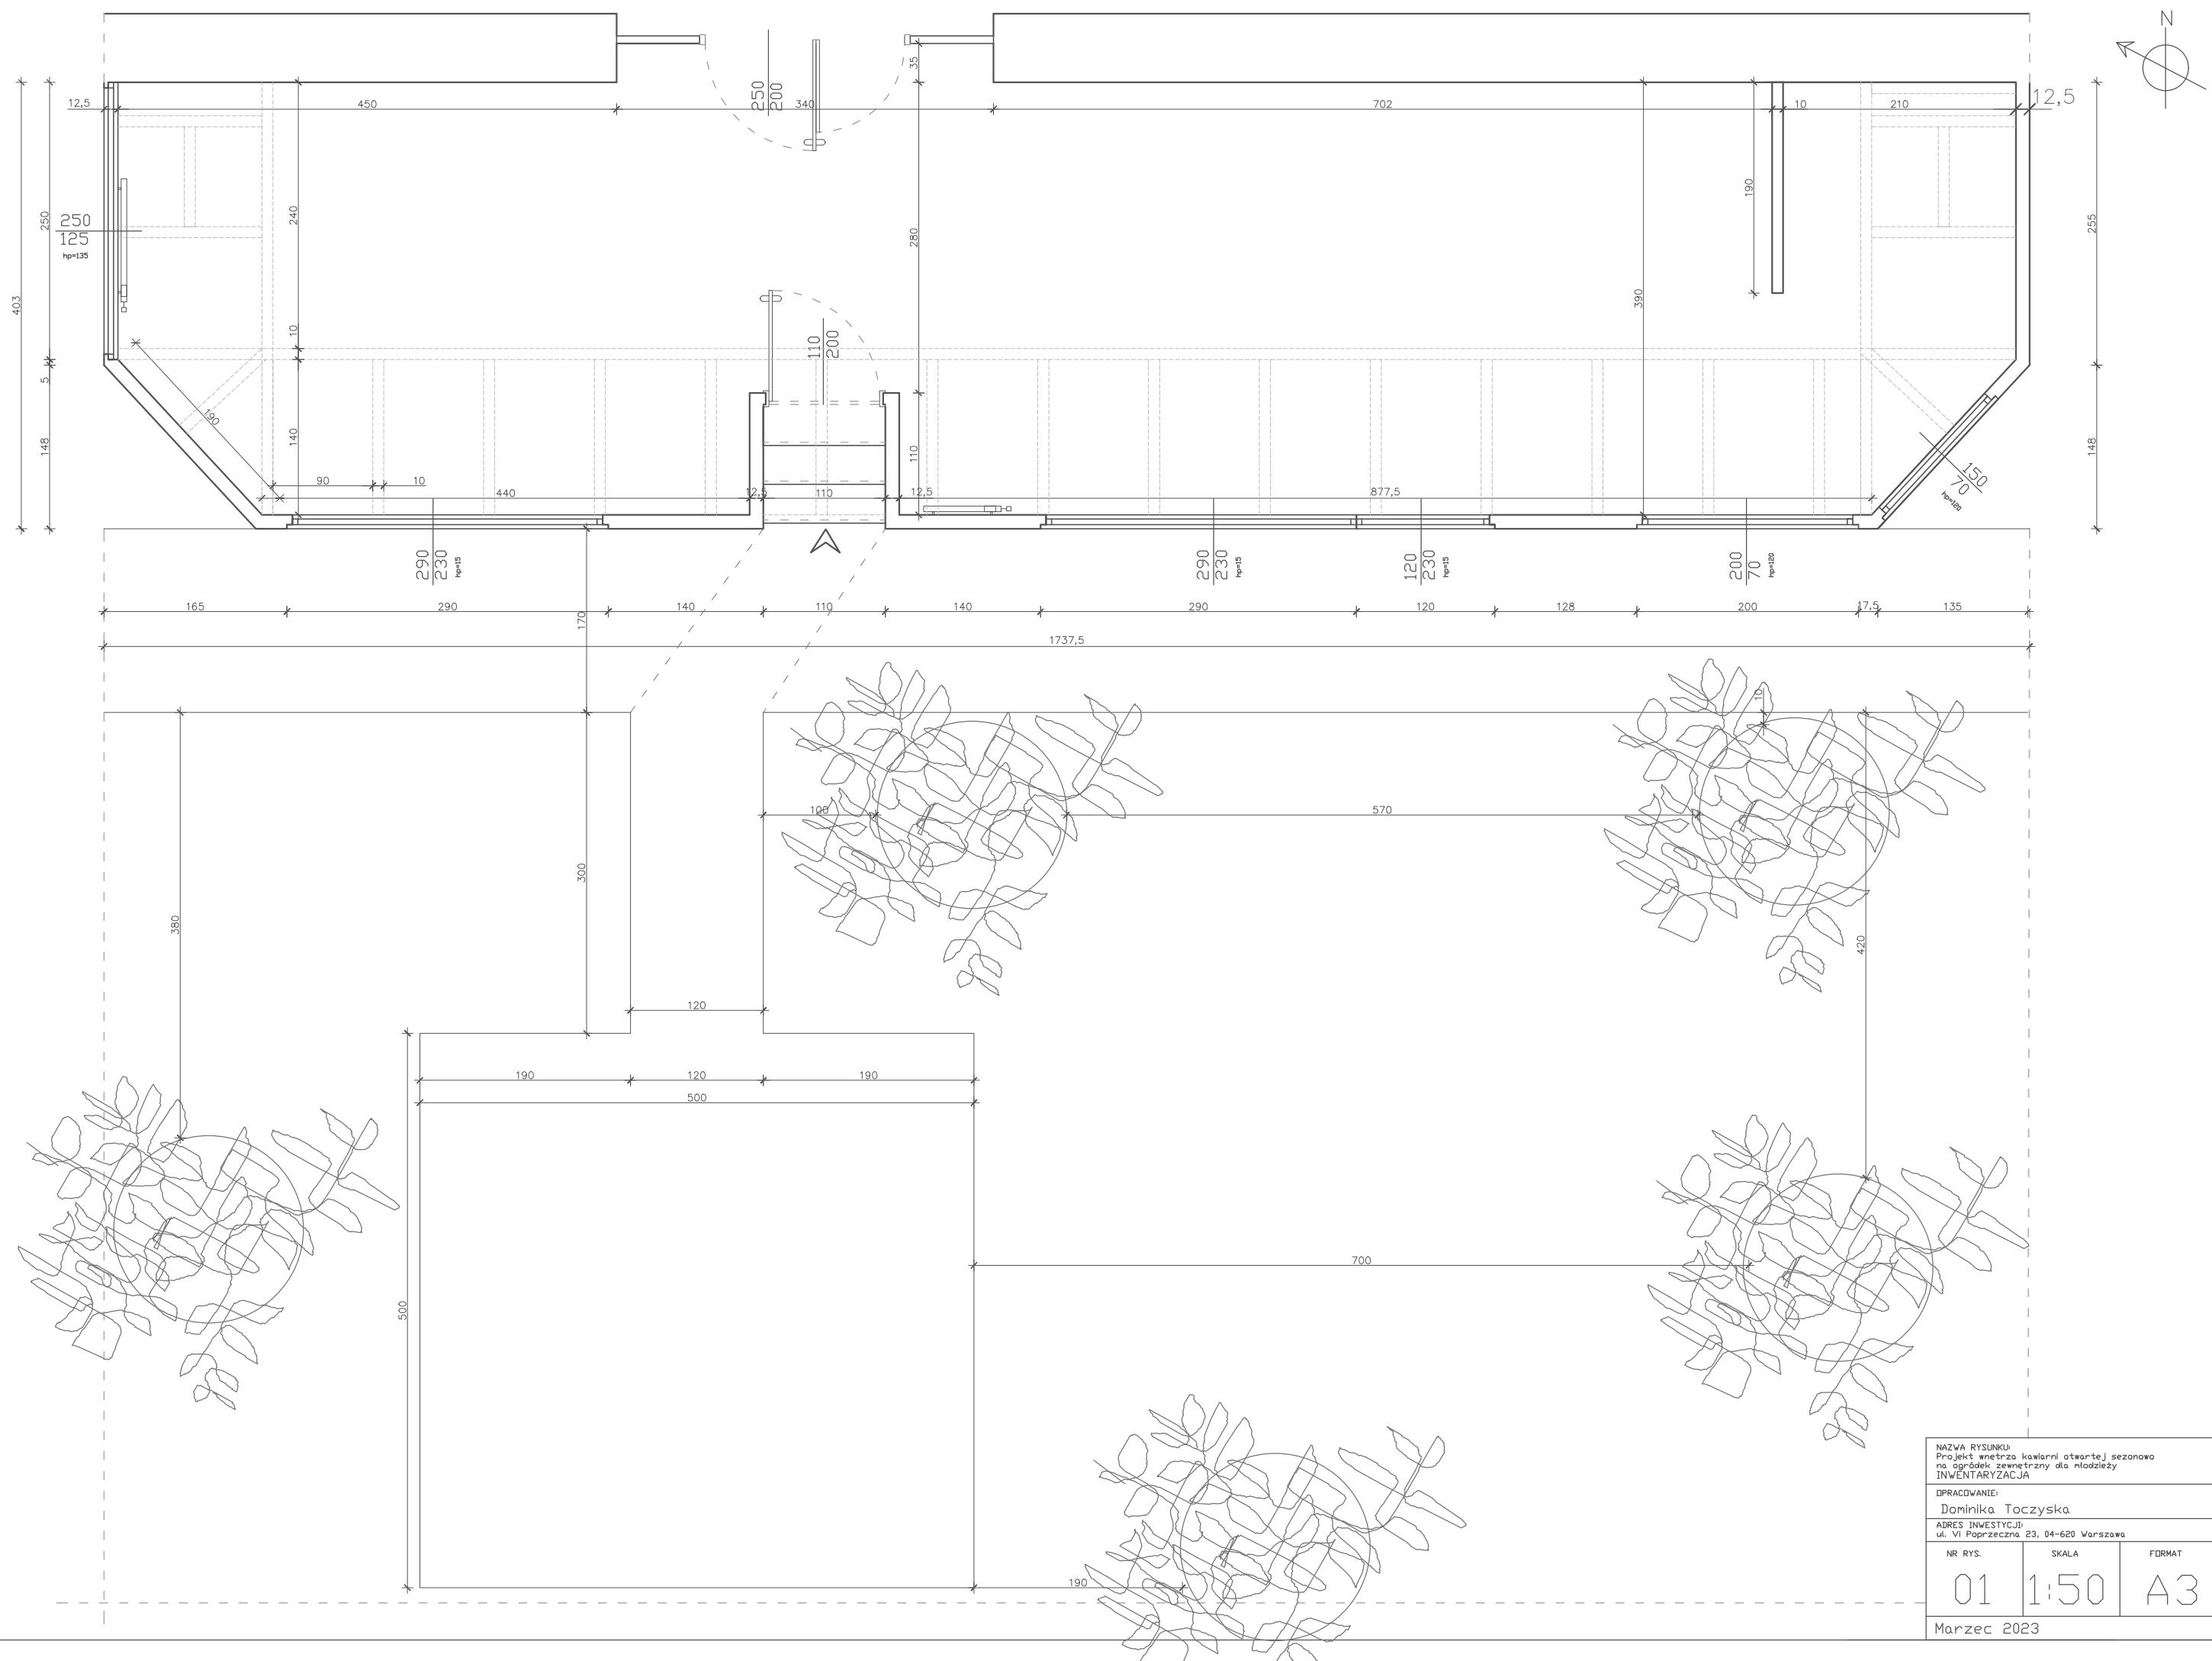


OZNACZENIA:

- ściany do wyburzenia
- ściany do postawienia

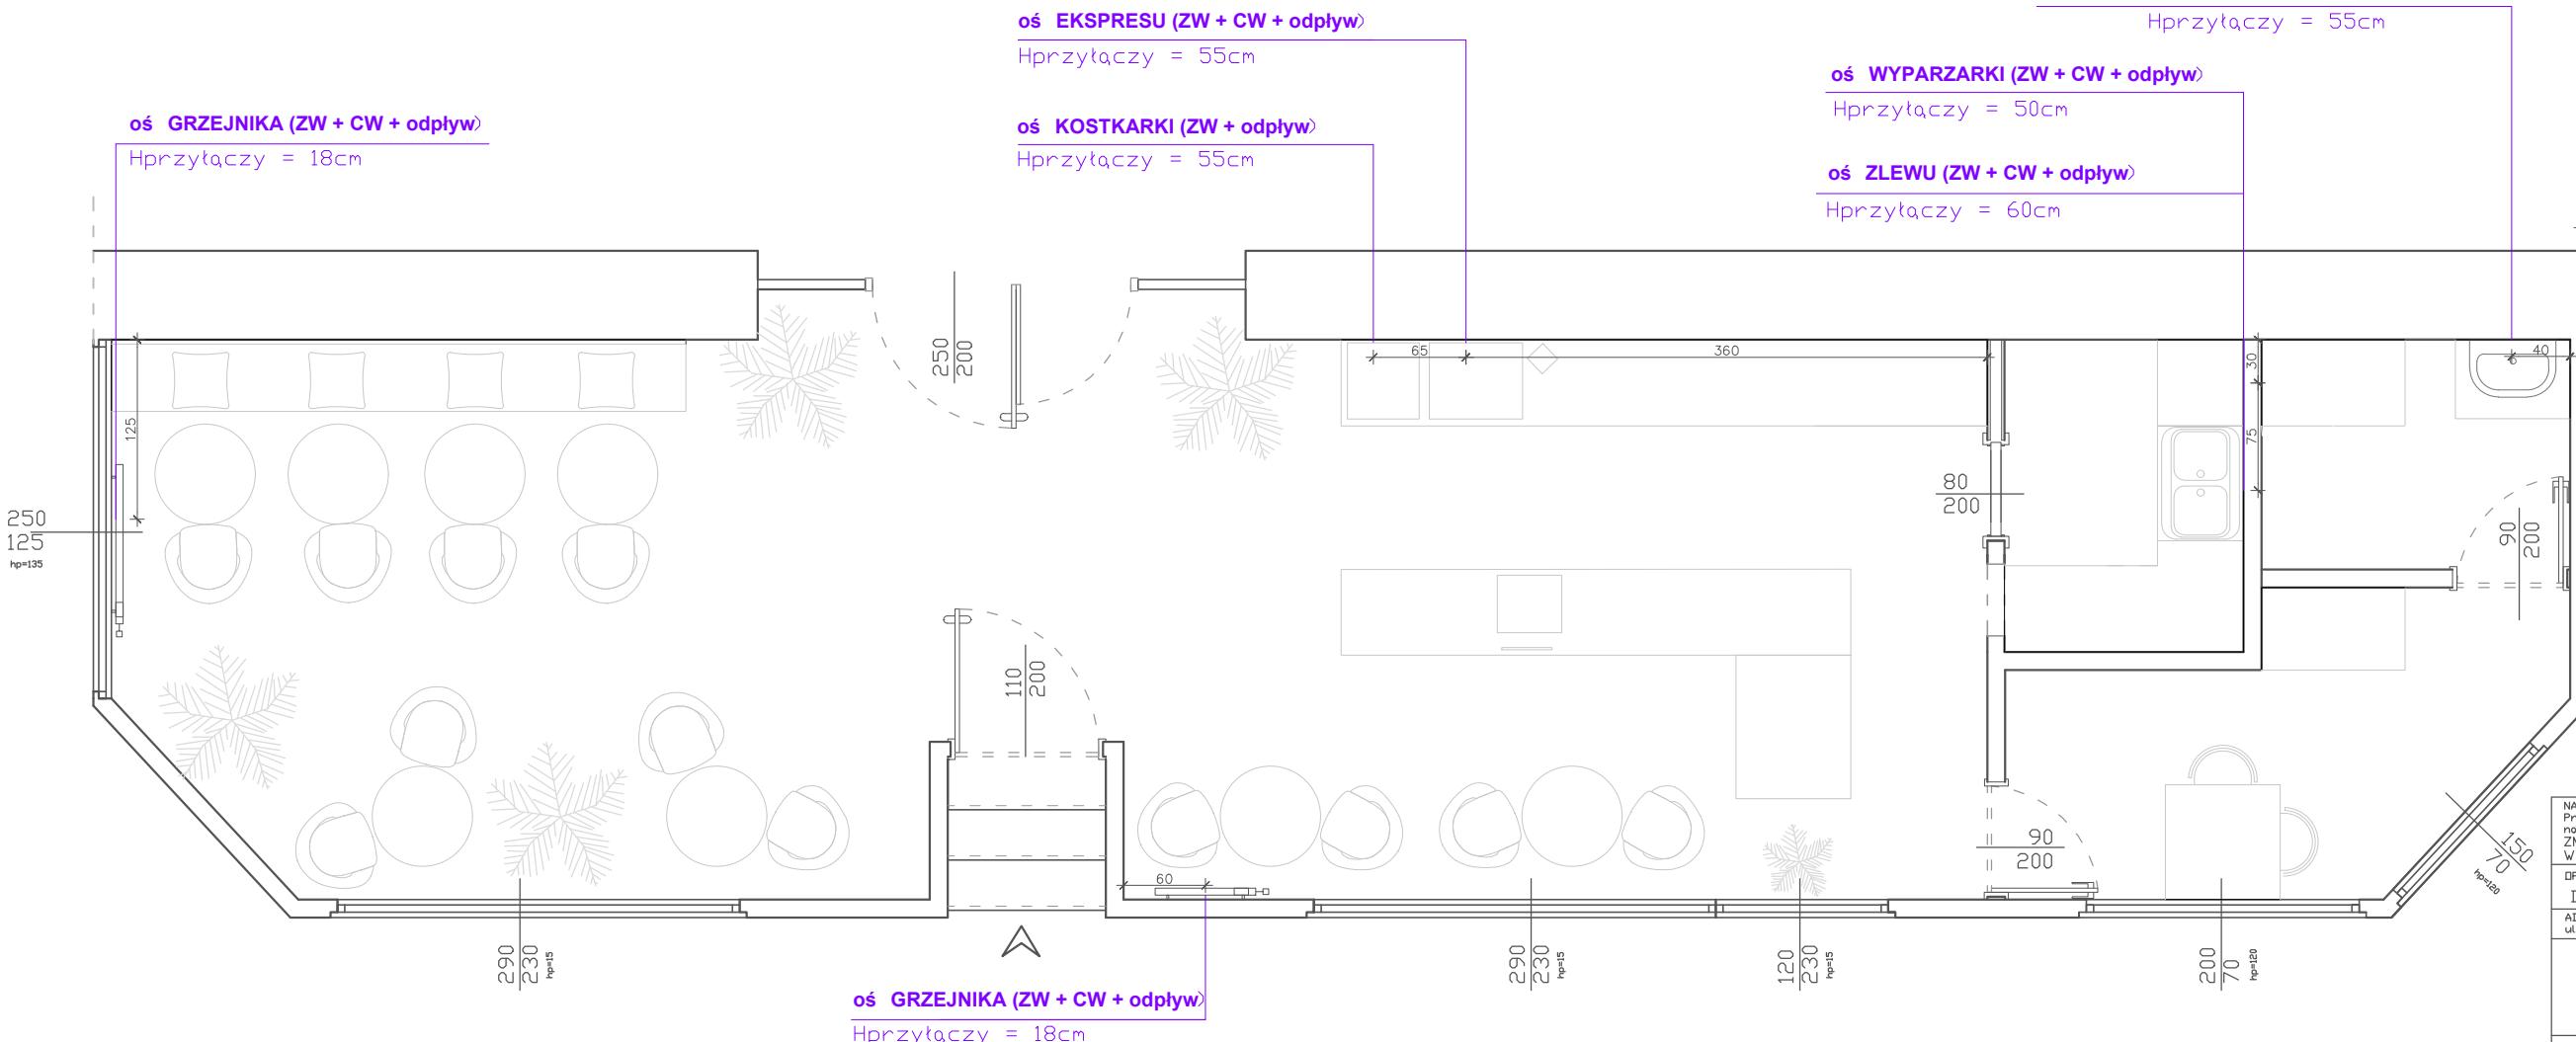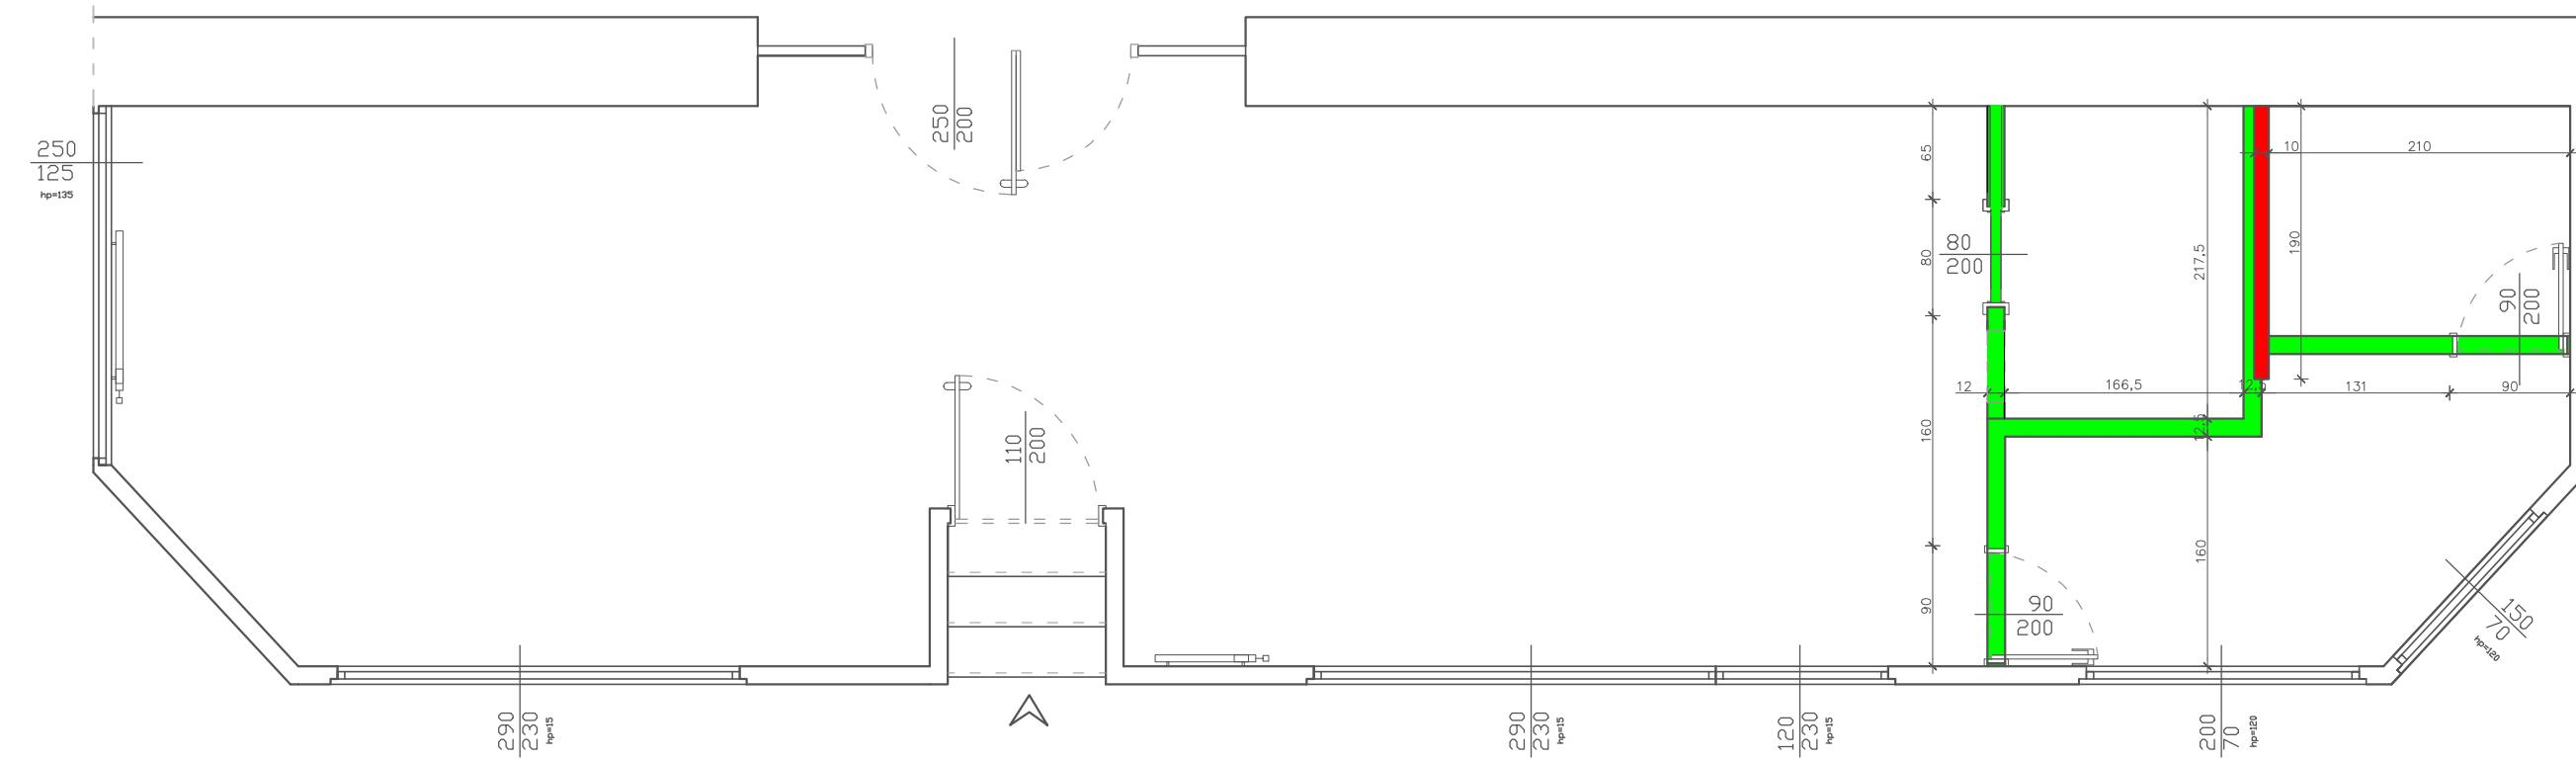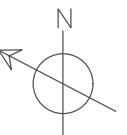

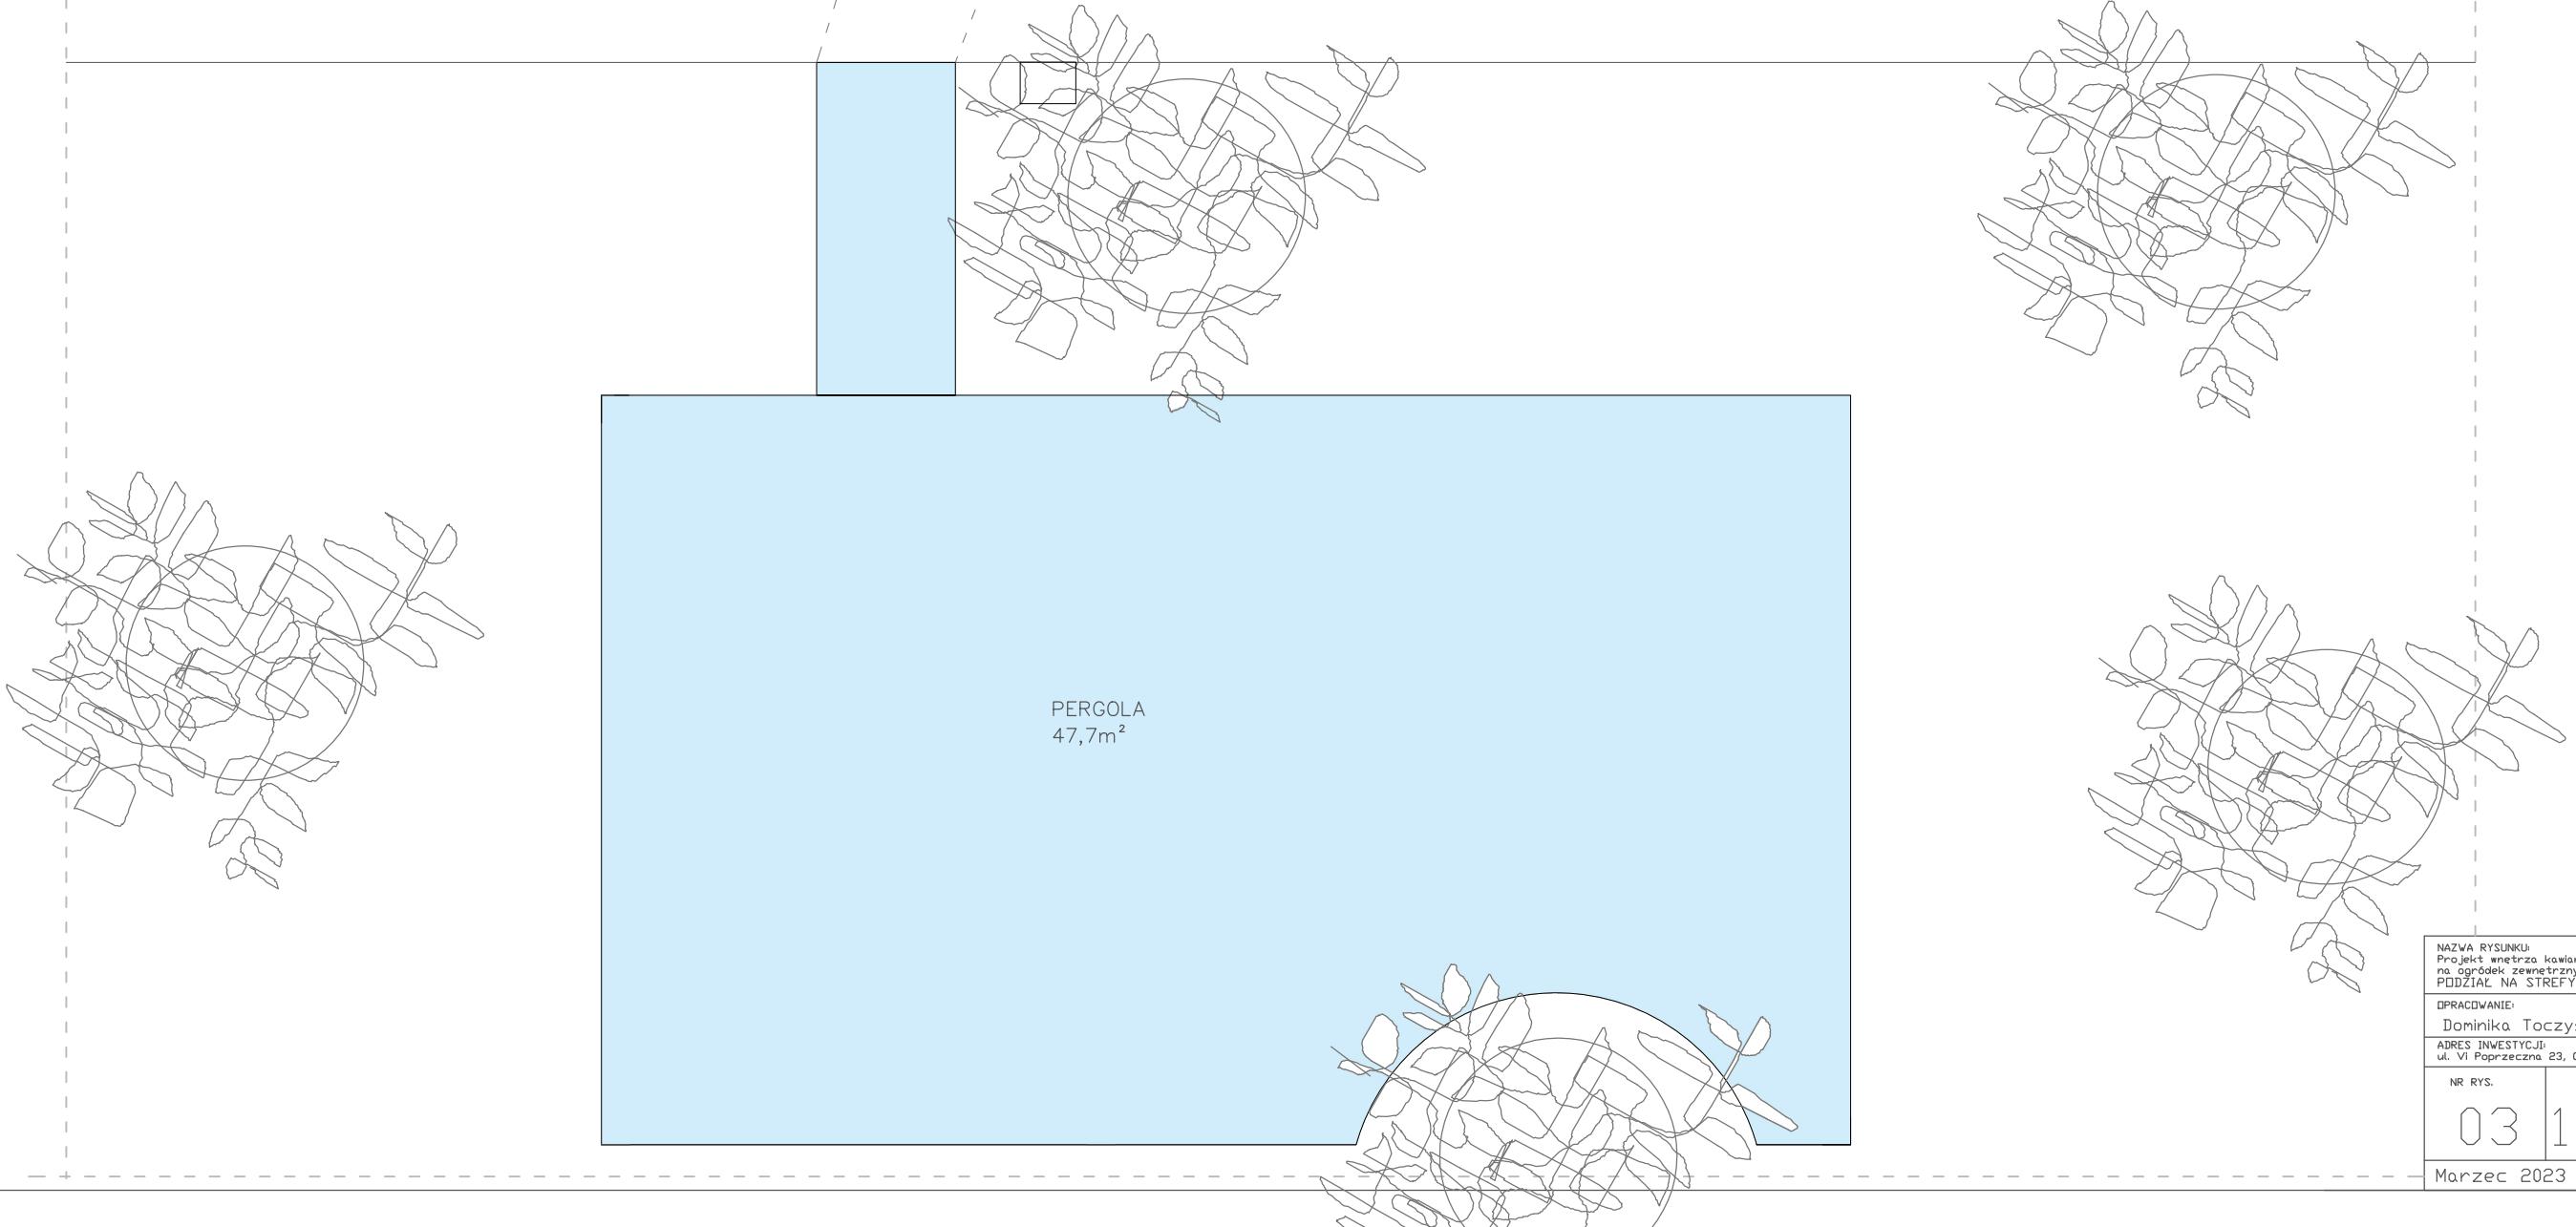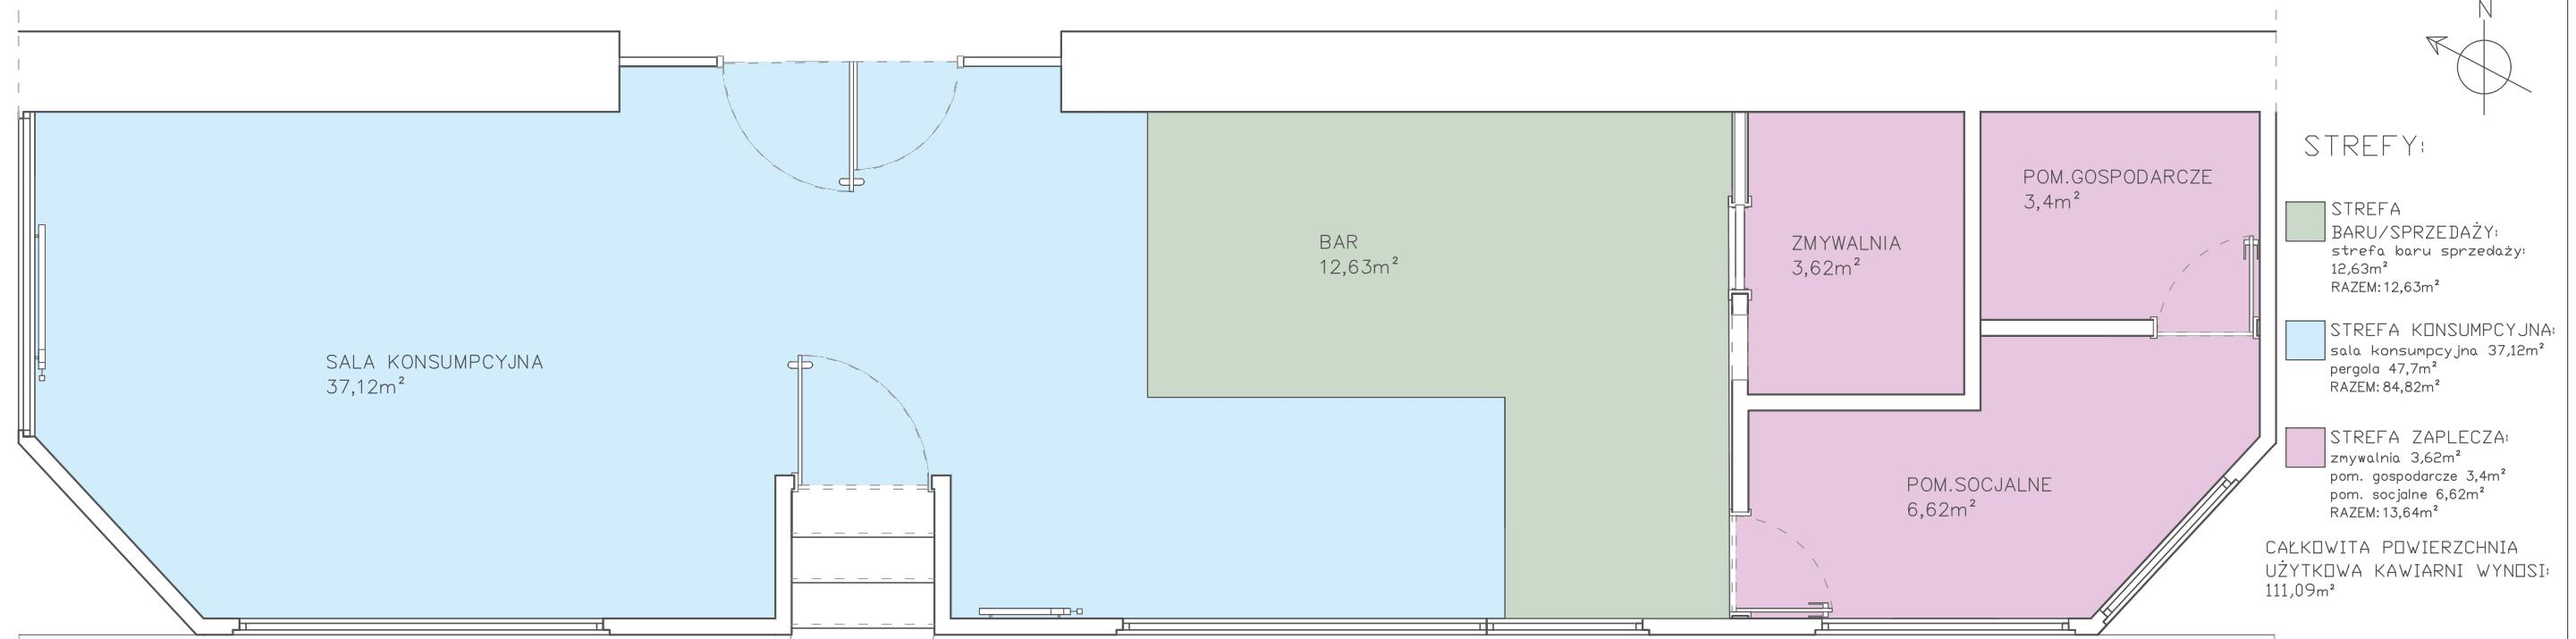

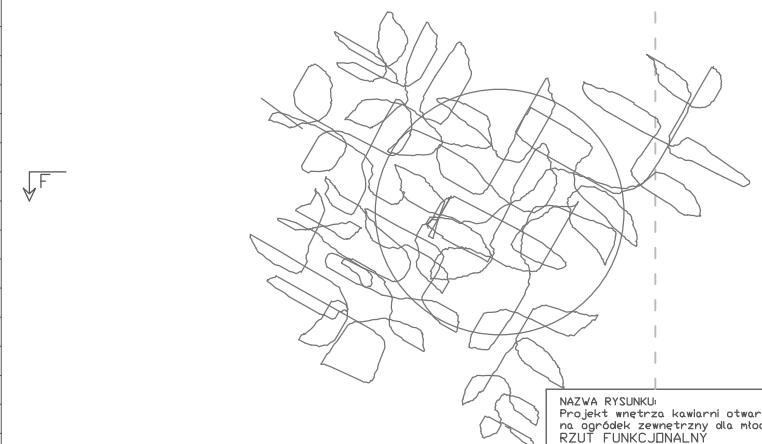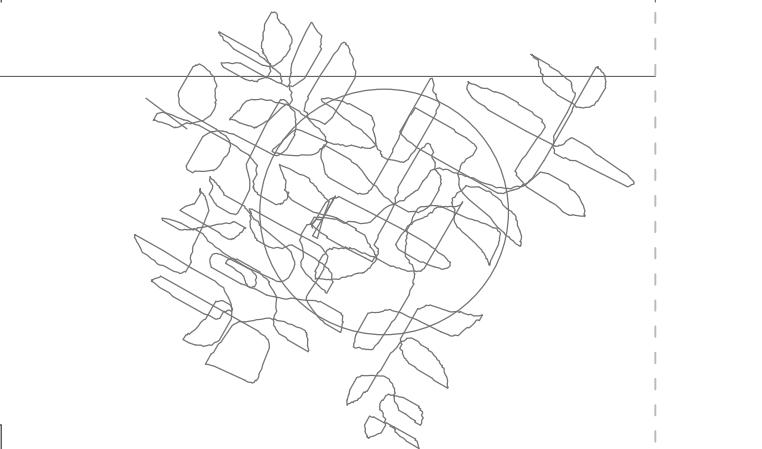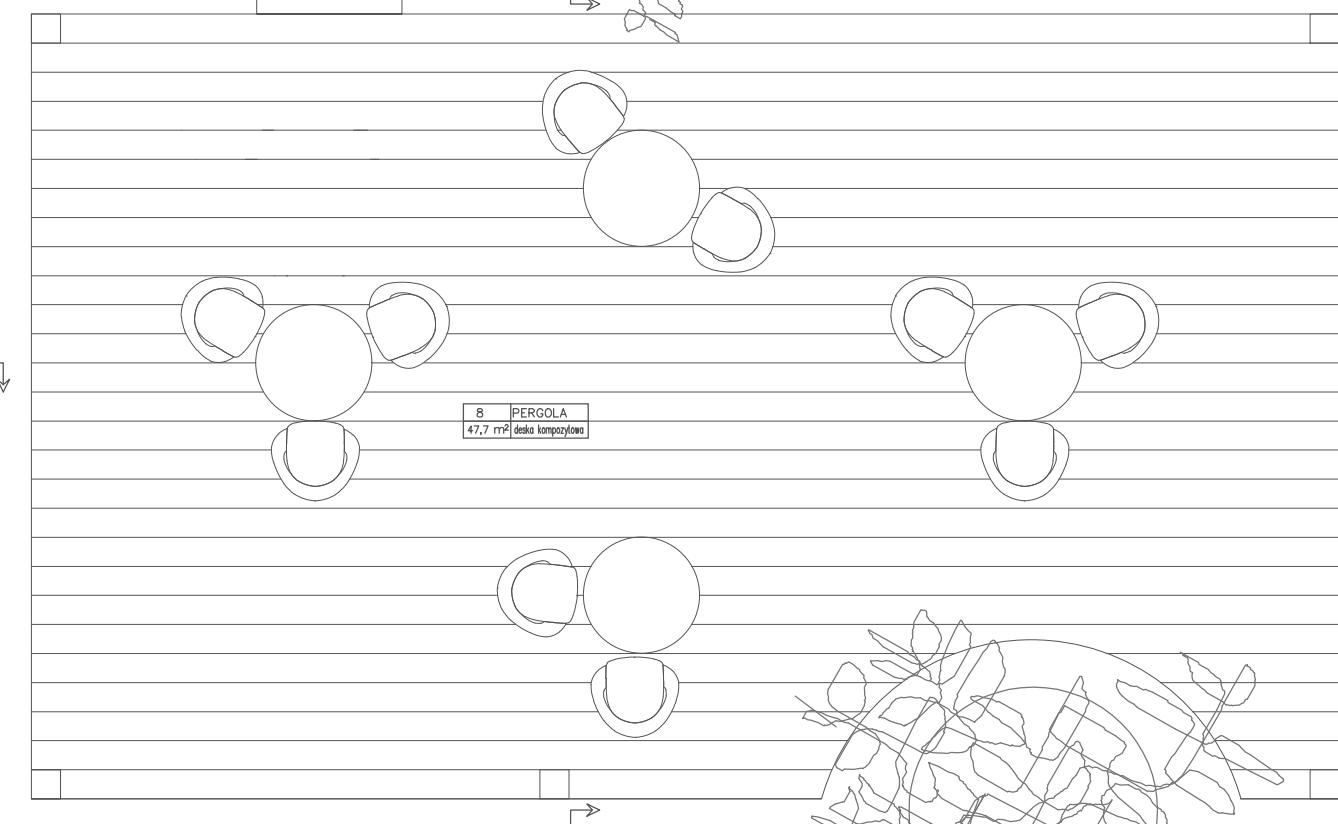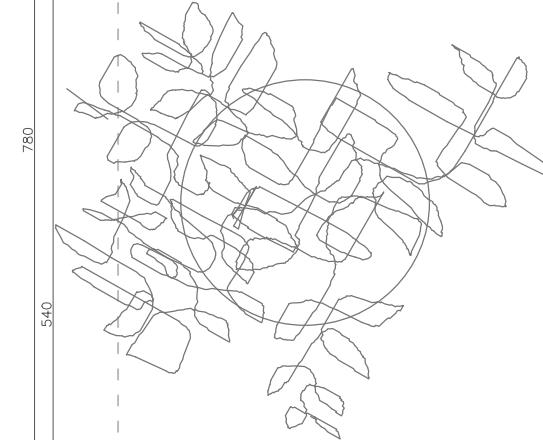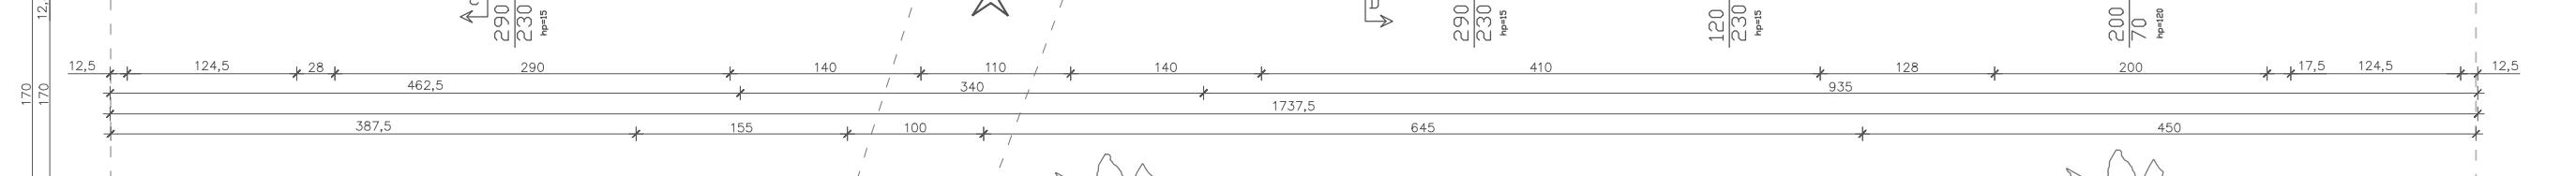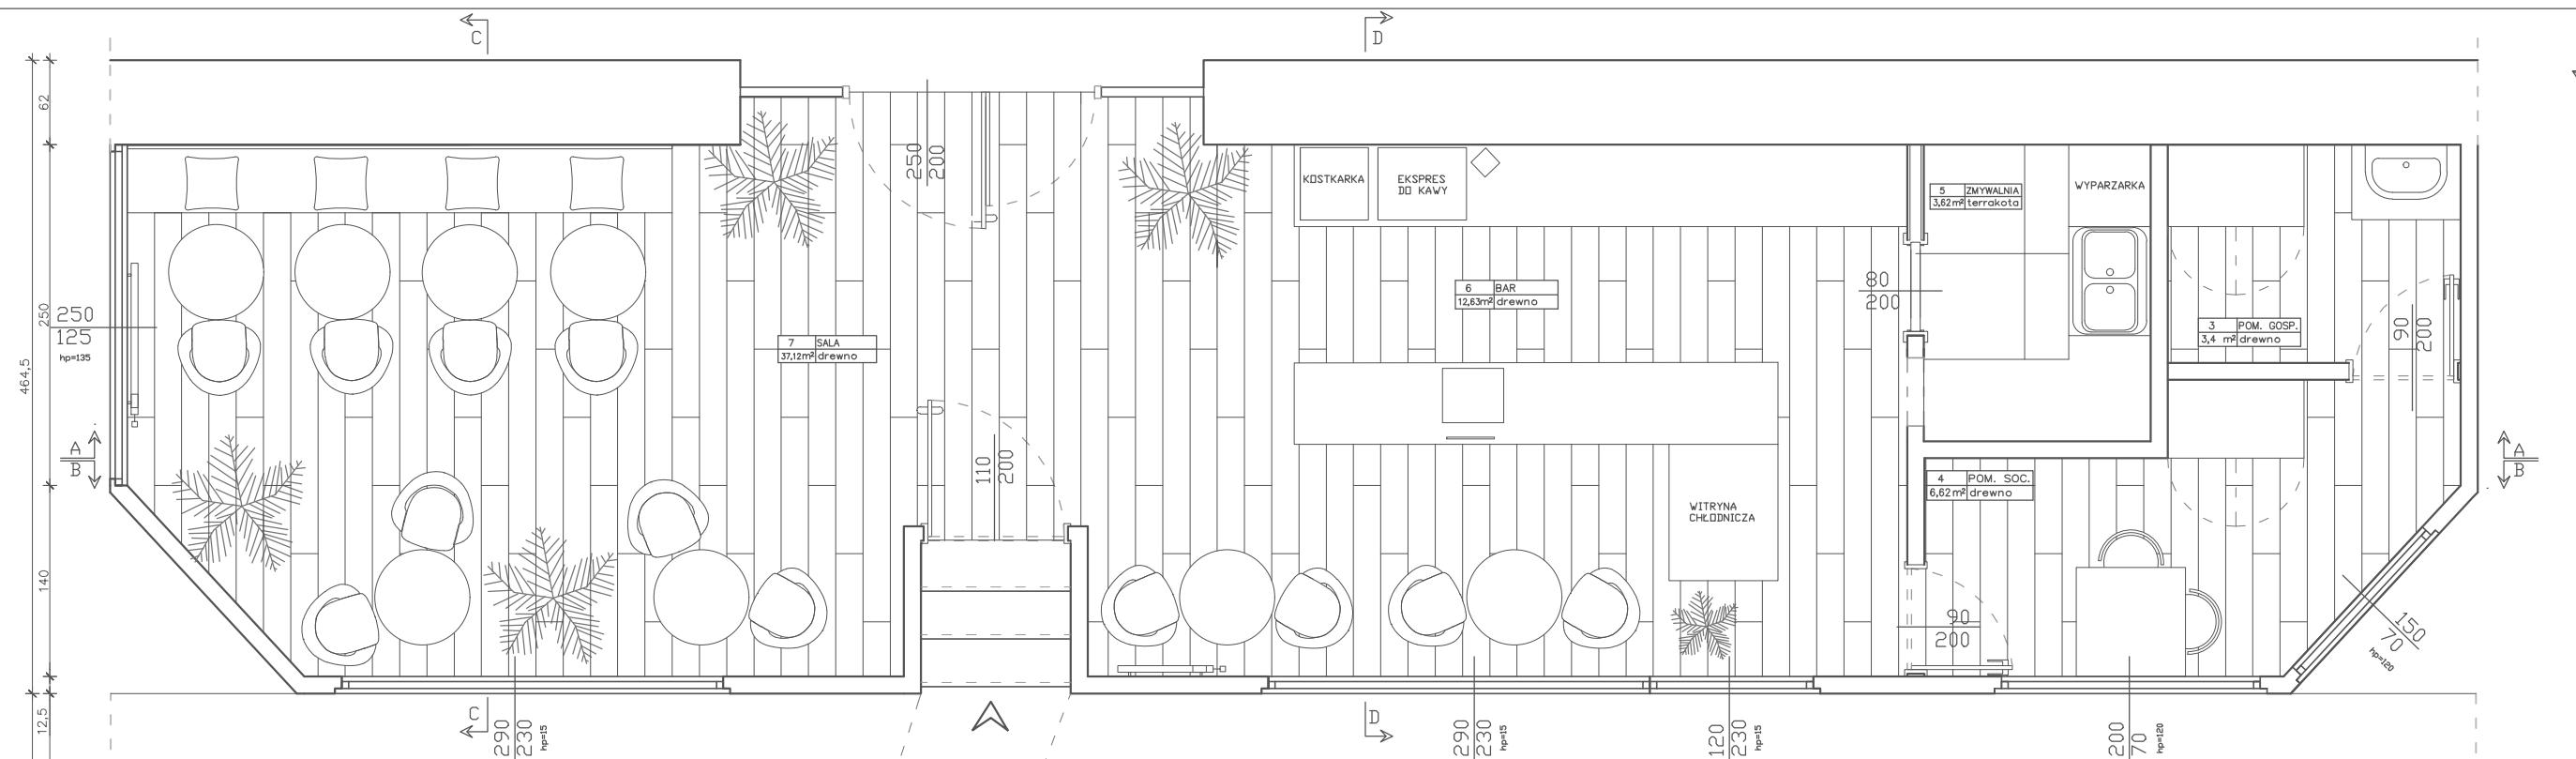


NAZWA RYSUNKU:
Projekt wnętrza kawiarni otwartej sezonowo
na ogródek zewnętrzny dla młodzieży
RZUT FUNKCJONALNY

DOPRACOWANIE:
Dominika Toczyńska

ADRES INWESTYCJI: ul. VI Poprzeczna 23, 04-620 Warszawa


NR RYS.	SKALA	FORMAT
04	1:50	A3

Marzec 2023

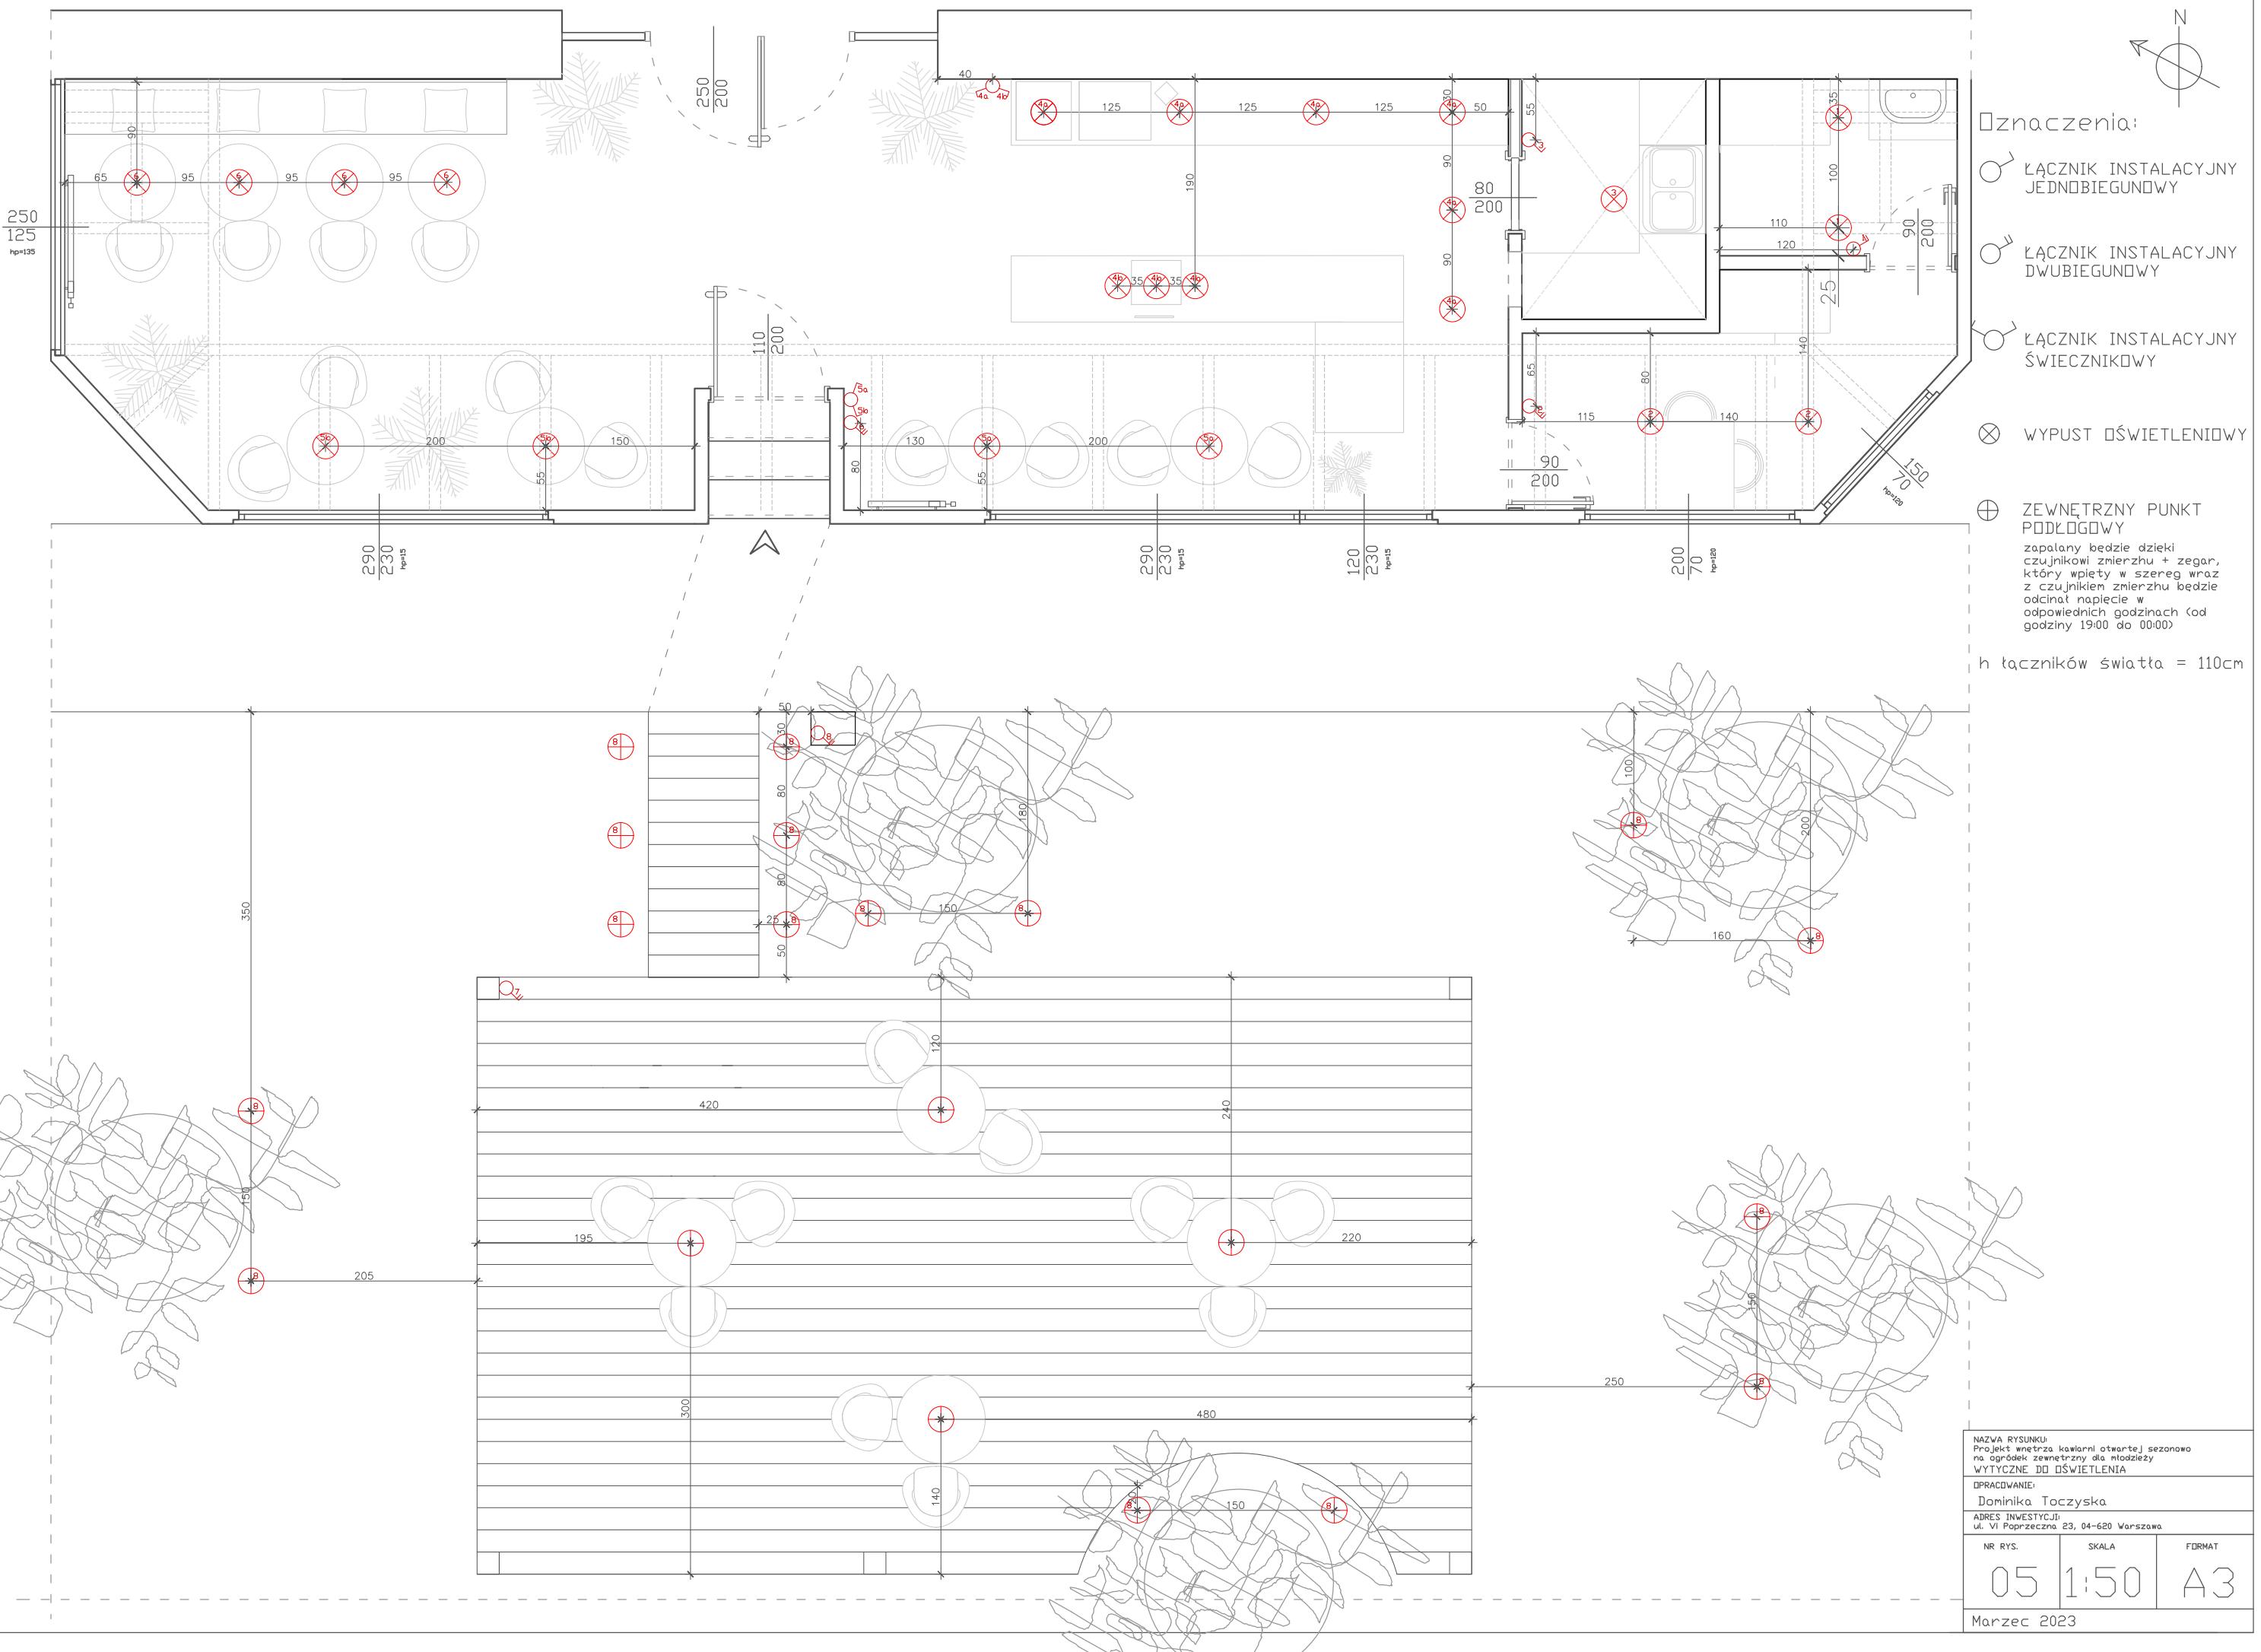


Oznaczenia:

- | | | | |
|--|--|--|---|
| | GNIAZDO WTYCZKOWE
ZE STYKIEM OCHRONNYM
16A/230V POJEDYNCZE, IP20 | | DO ŁODÓWKI |
| | GNIAZDO WTYCZKOWE
ZE STYKIEM OCHRONNYM
16A/230V PODWÓJNE, IP20 | | DO EKSPRESU |
| | GNIAZDO WTYCZKOWE
ZE STYKIEM OCHRONNYM
16A/230V PODWÓJNE, IP20 | | DO KOSTKARKI |
| | GNIAZDO WTYCZKOWE HERMETYCZNE
ZE STYKIEM OCHRONNYM
16A/230V POJEDYNCZE, IP20 | | GNIAZDO CHOWANE W
PODŁÓGE/BLAT |
| | GNIAZDO WTYCZKOWE
HERMETYCZNE DO WYPARZARKI | | GNIAZDO WTYCZKOWE Z
CZUJNIKIEM ZMIERZCHU
16A/230, PODWÓJNE IP20 |

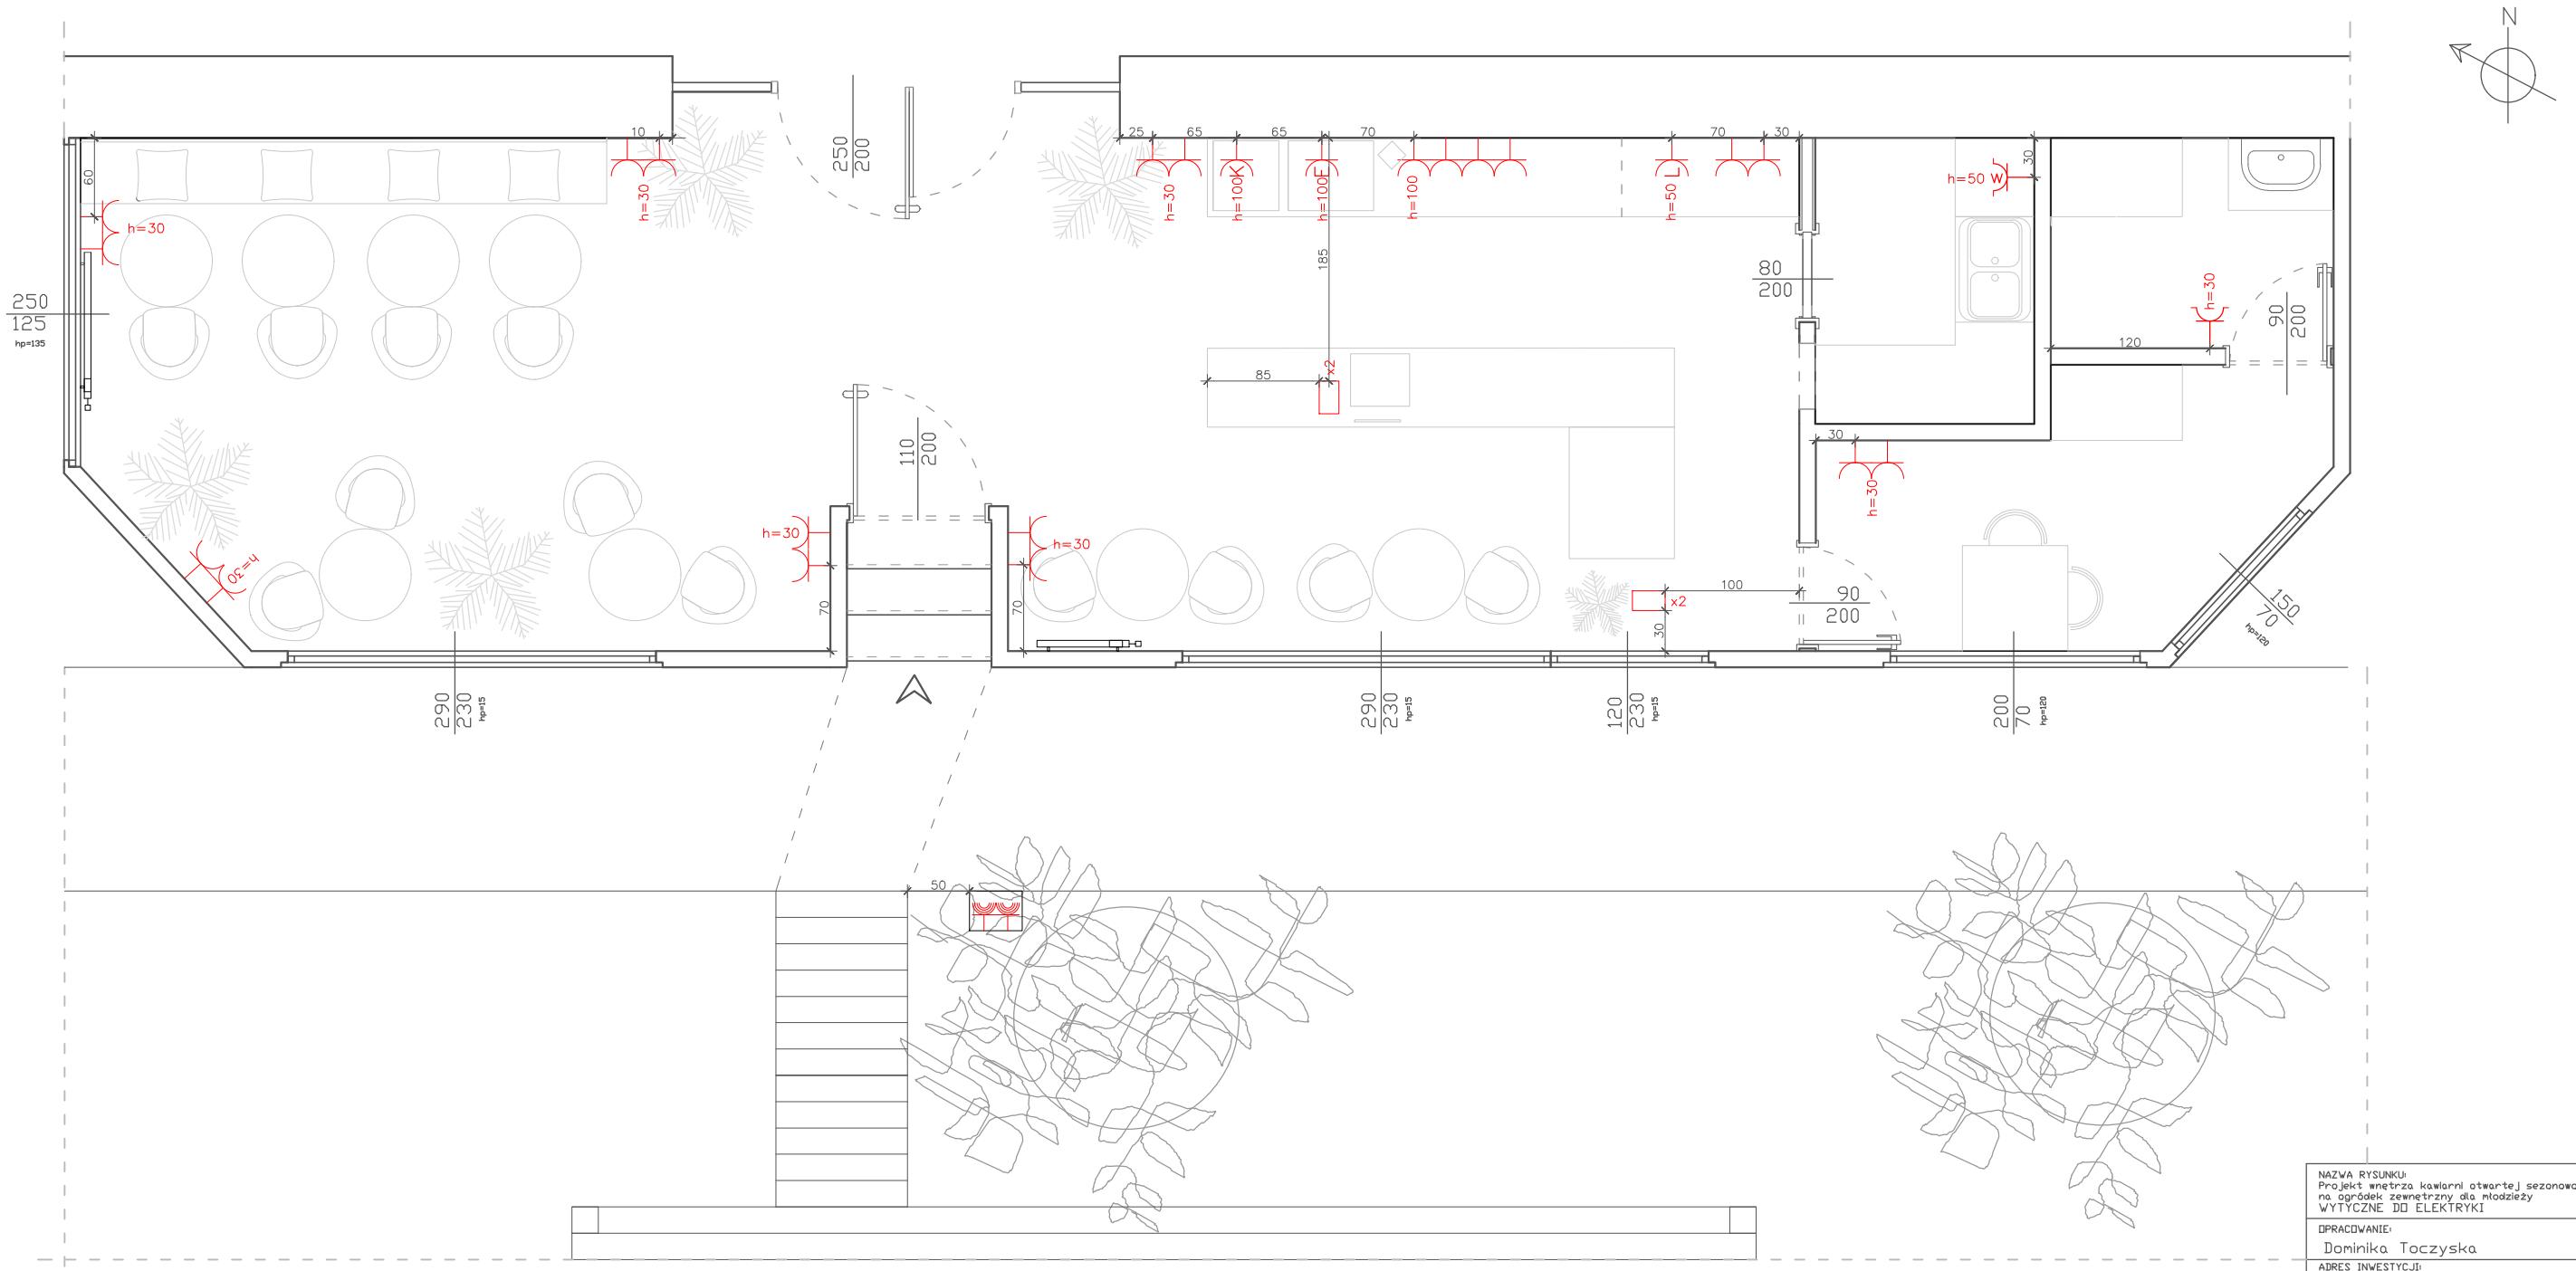

<p>NAZWA RYSUNKU: Projekt wnętrza kawiarni otwartej sezonowo na ogródzie zewnętrzny dla młodzieży WYTYCZNE DO ELEKTRYKI</p> <p>OPRAWOCZANIE: Dominika Toczska</p> <p>ADRES INWESTYCJI: ul. V. Poprzeczna 23, 04-620 Warszawa</p>		
NR RYS.	SKALA	FORMAT
06	1:50	A3
Marzec 2023		

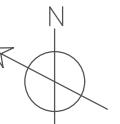

Oznaczenia:

Dąb Ciepły
Brązowy
Clm5789 Classic






Blanco Natural
80x80 biały
gres mat

Listwa
przypodłogowa
blata z
wodoodpornej
powłoką-MDF
lakierowany
biały RAL9003




Na zewnątrz:

Deska tarasowa
Dąbowa

Kierunek
kładzenia
płytek

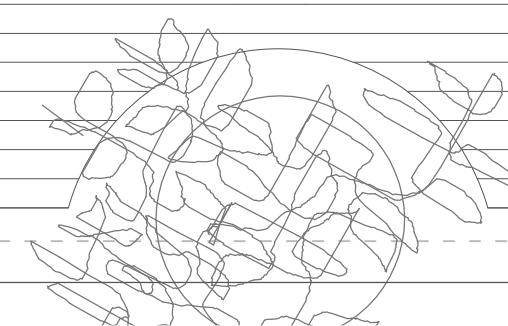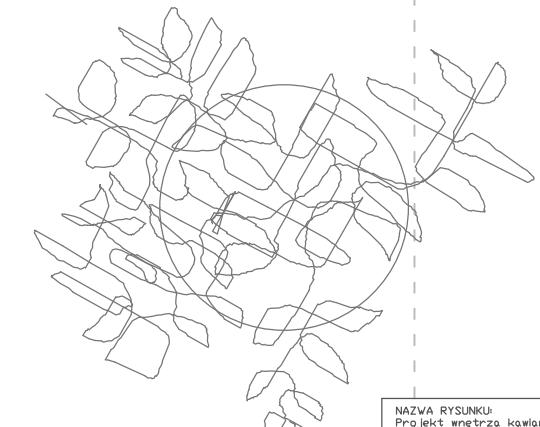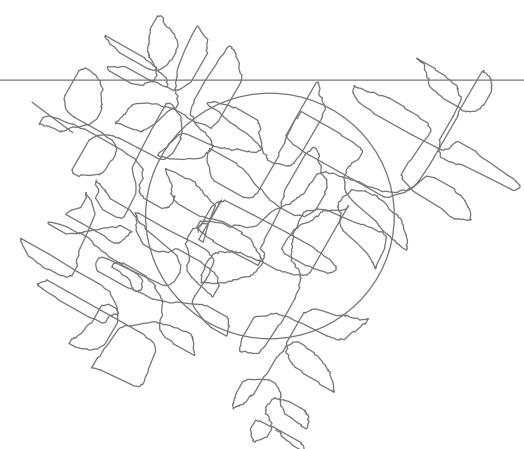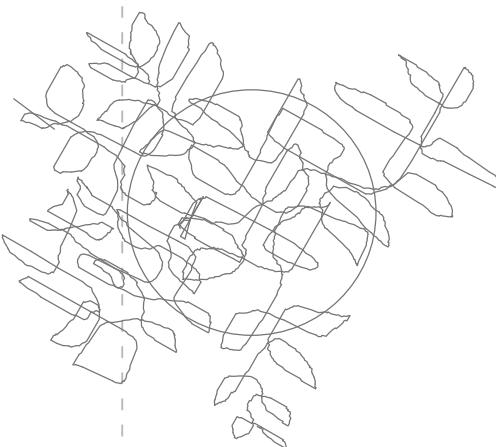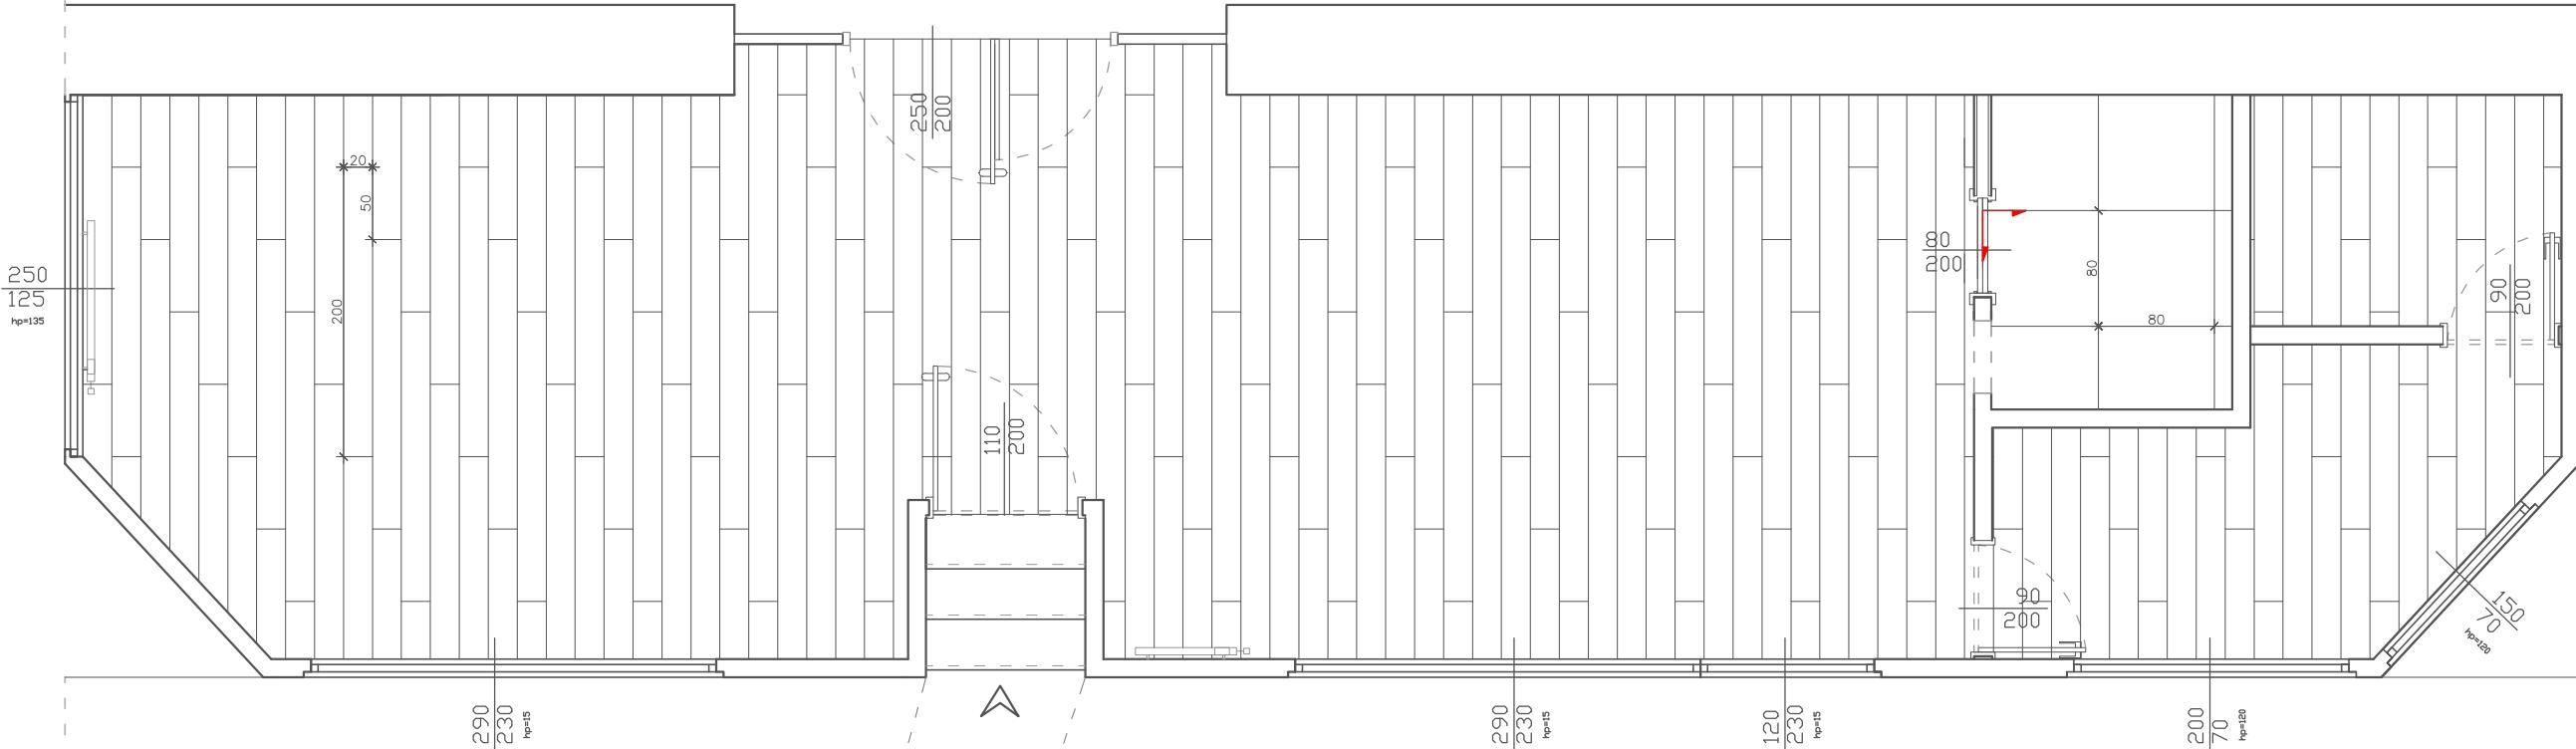

NAZWA RYSUNKU: Projekt wnętrza kawiarni otwartej sezonowo na ogródek zewnętrzny dla młodzieży RZUT PODŁOGI		
OPRACOWANIE: Dominika Toczyńska		
ADRES INWESTYCJI: ul. VI Poprzeczna 23, 04-620 Warszawa		
NR RYS.	SKALA	FORMAT
07	1:50	A3
Marzec 2023		

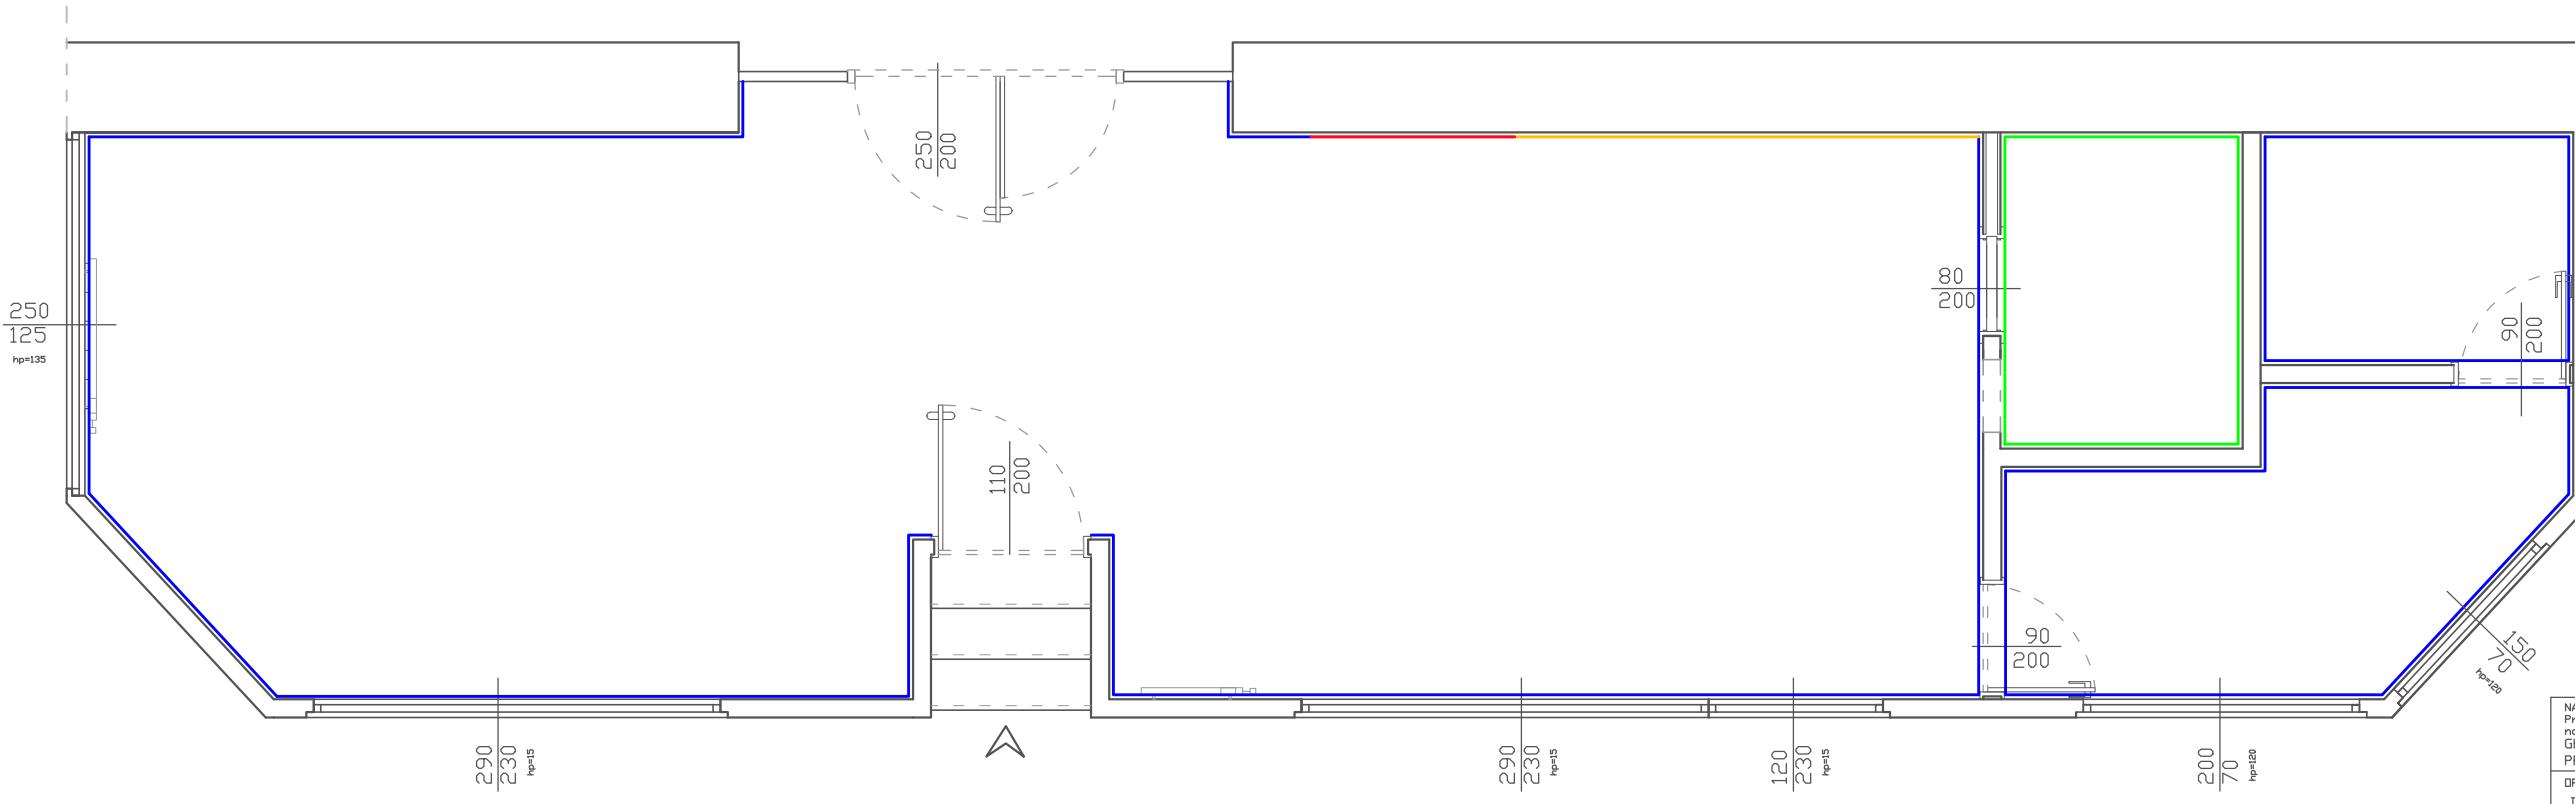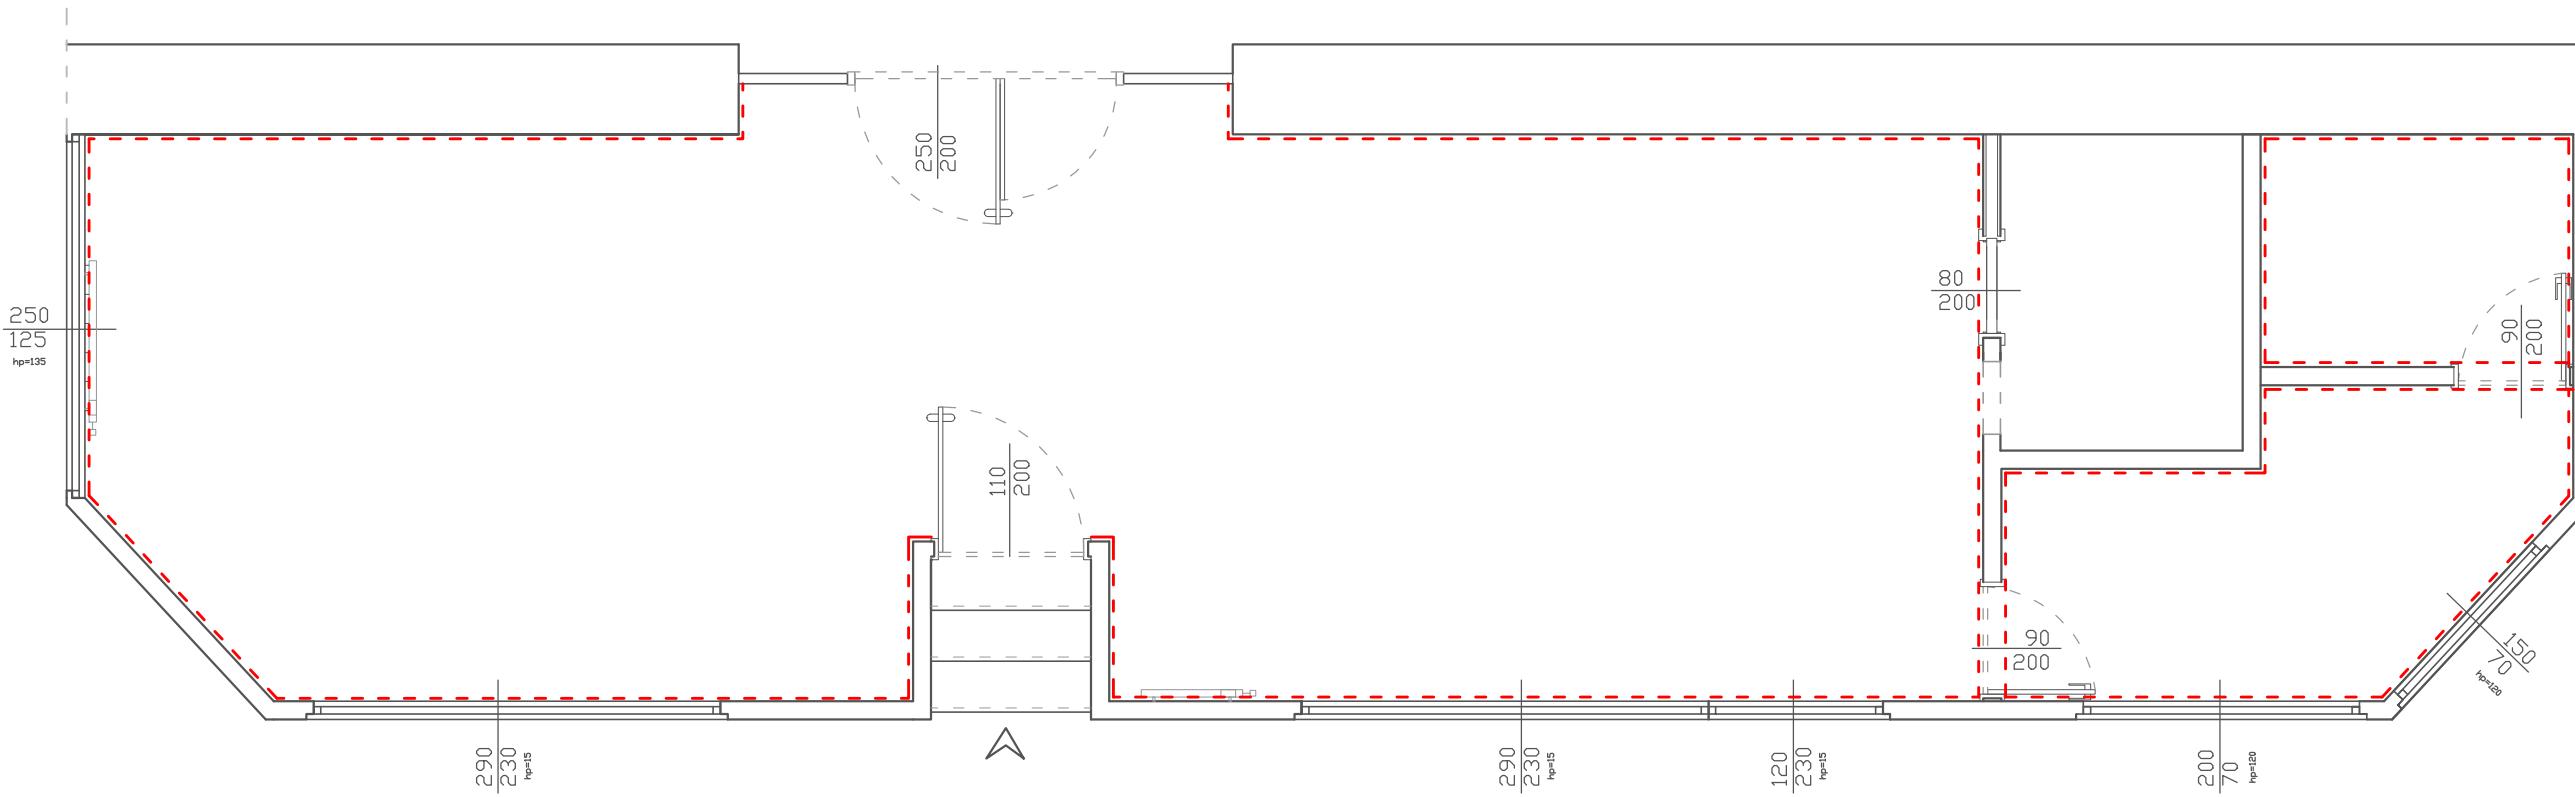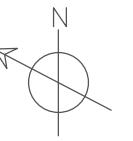





NAZWA RYSUNKU:
Projekt wnętrza kawiarni otwartej sezonowo
na ogródek zewnętrzny dla młodzieży
GŁADZIE
PROJEKT MALOWANIA ŚCIAN

OPRACOWANIE:
Dominika Toczyńska

ADRES INWESTYCJI:
ul. VI Poprzeczna 23, 04-620 Warszawa

NR RYS. SKALA FORMAT
08 1:50 A3

Marzec 2023

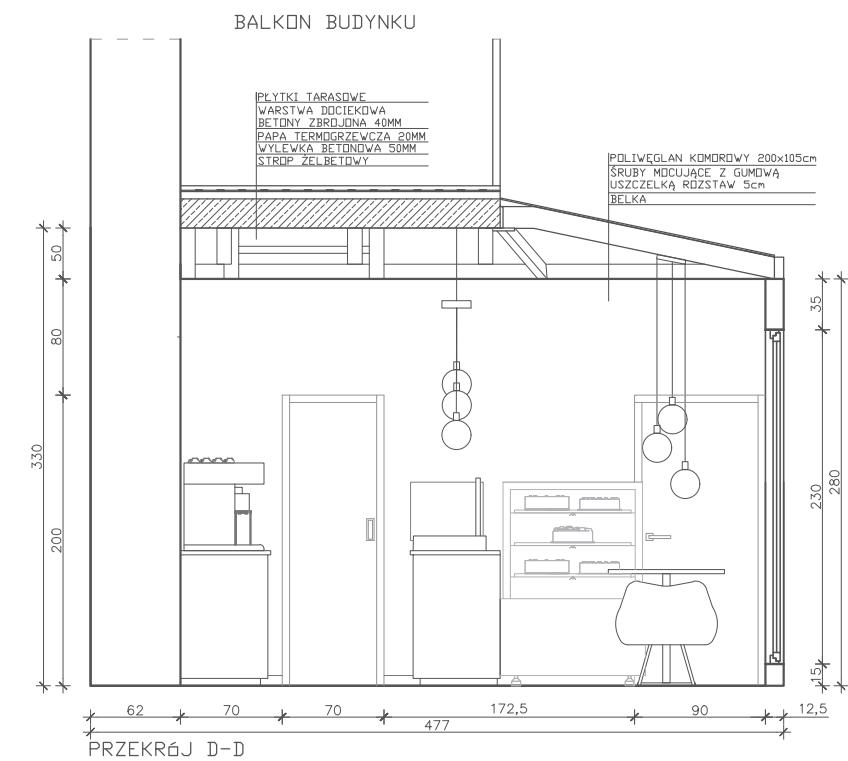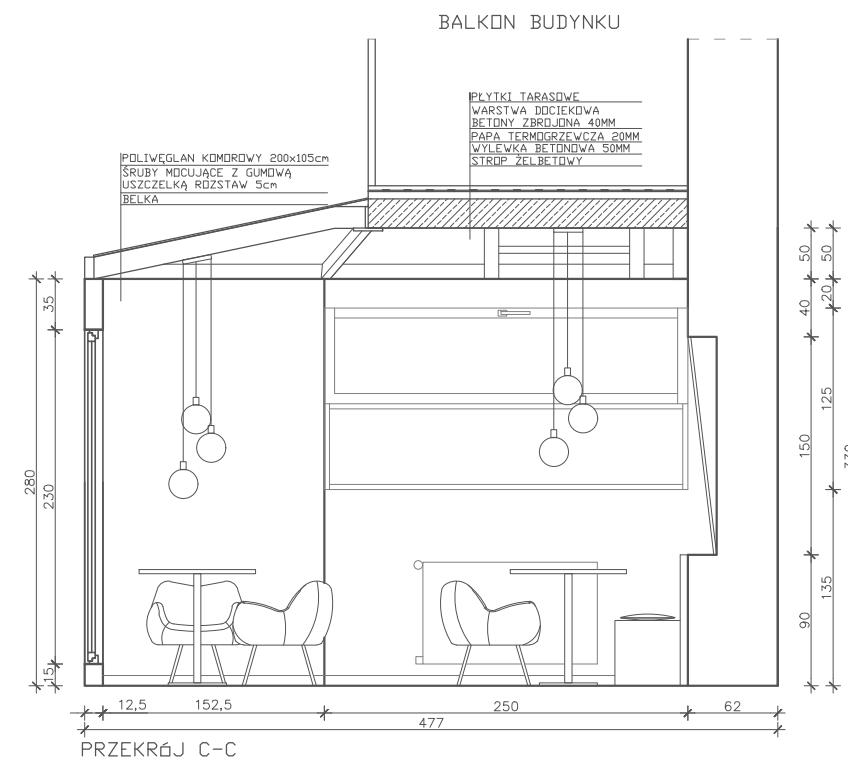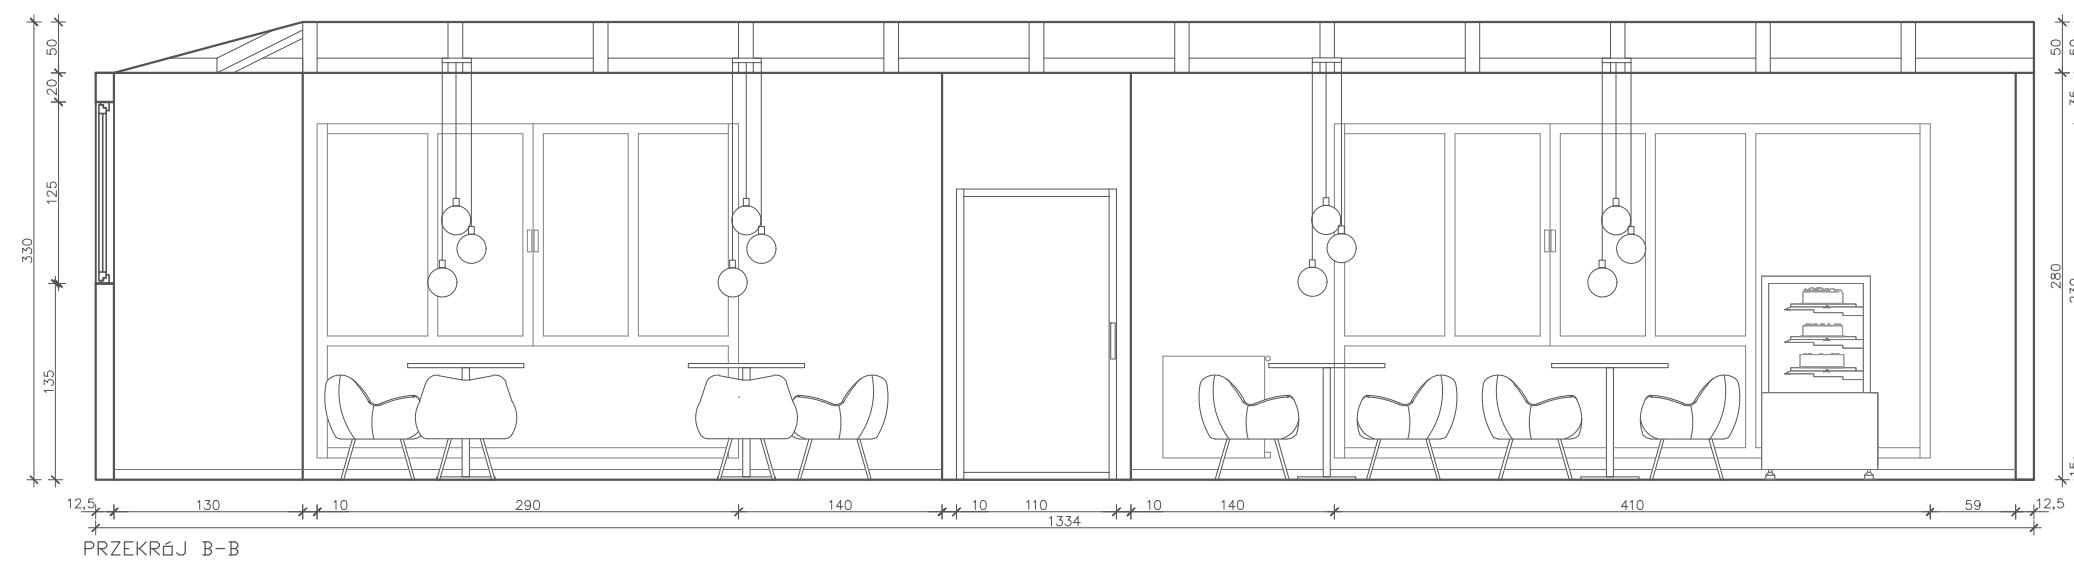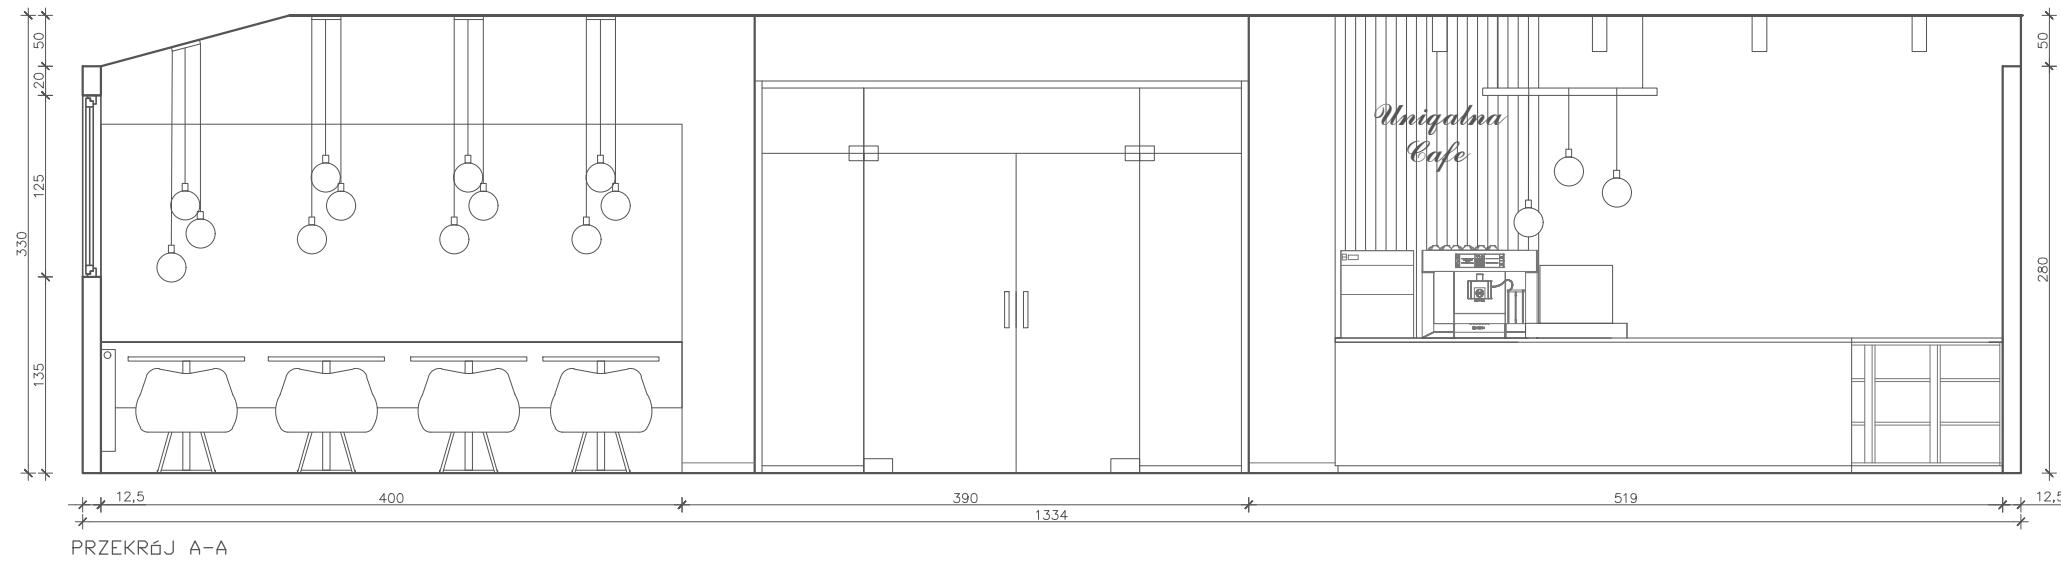


NAZWA RYSUNKU:
Projekt wnętrza kawiarni otwartej sezonowo
na ogródek zewnętrzny dla młodzieży
PRZEKRÓJE A-A, B-B, C-C, D-D

OPRACOWANIE:
Dominika Toczyńska


ADRES INWESTYCJI:
ul. VI Poprzeczna 23, 04-620 Warszawa

NR RYS.	SKALA	FORMAT
09	1:50	A3


Marzec 2023

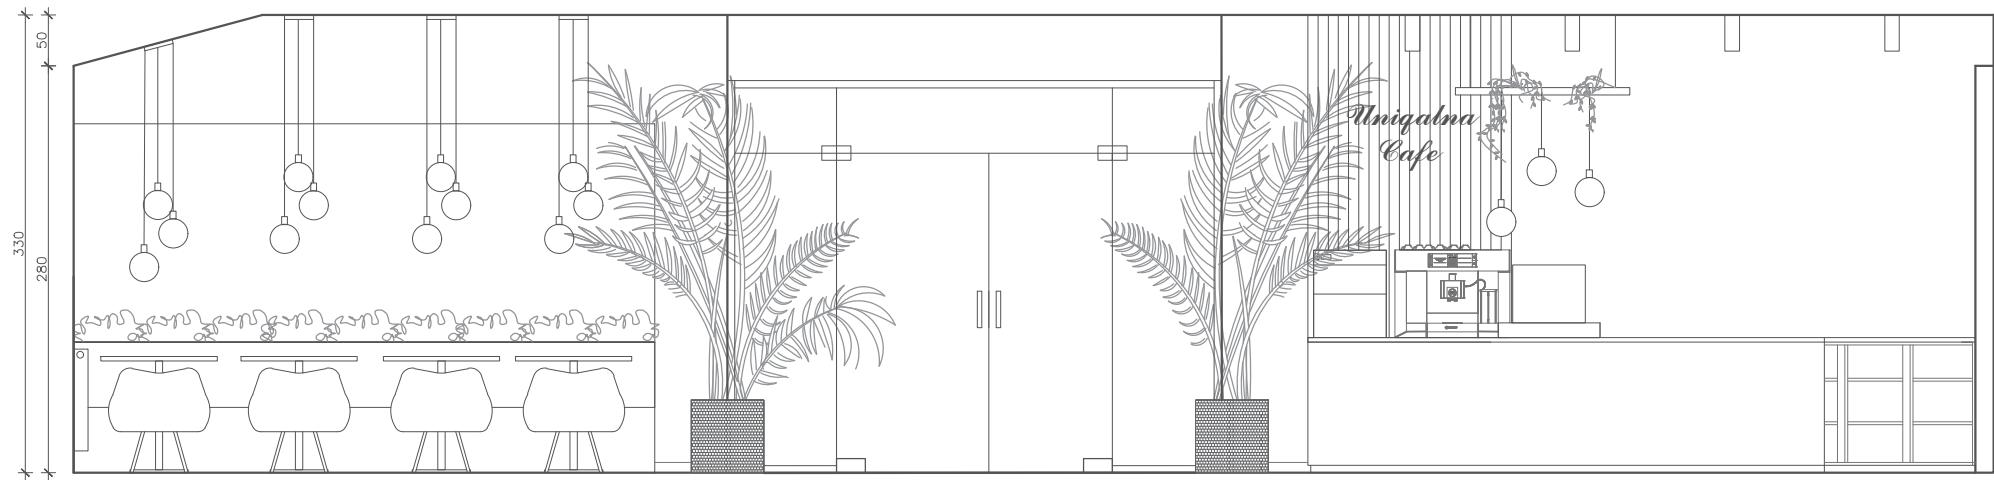


WIDOK A-A

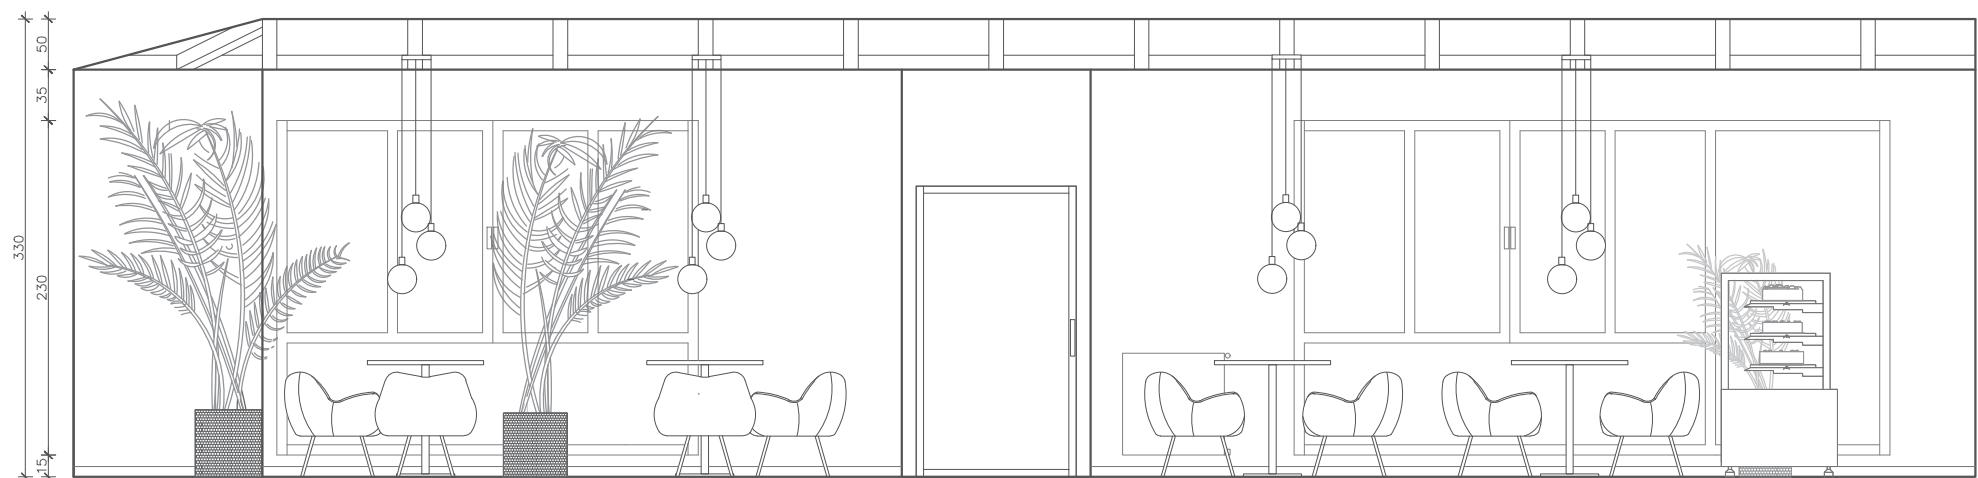

WIDOK B-B

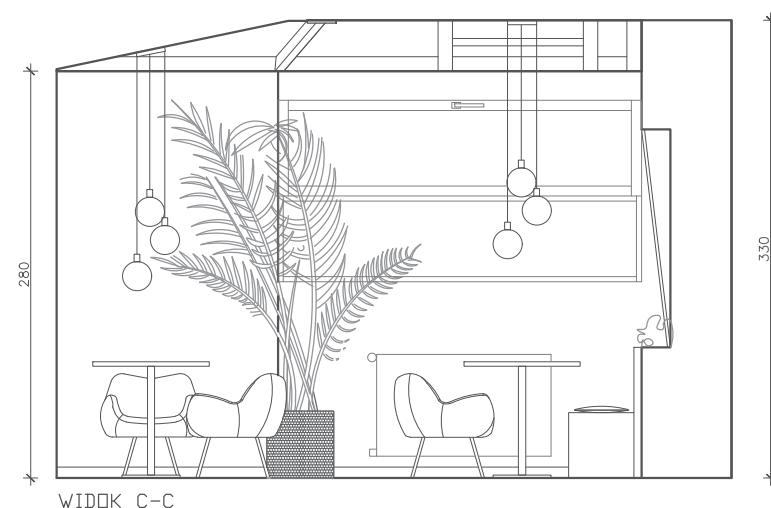


WIDOK C-C

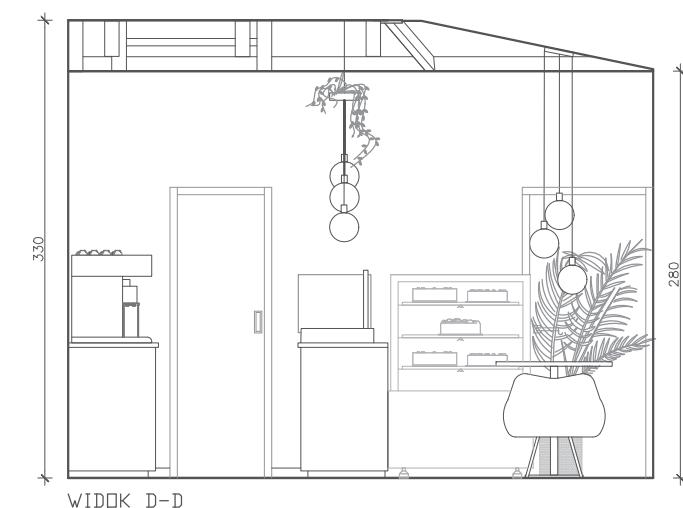


WIDOK D-D

NAZWA RYSUNKU: Projekt aneksu kawiarni otwartej sezonowo na ogródek zewnętrzny dla młodzieży WIDOKI A-A, B-B, C-C, D-D		
OPRACOWANIE: Dominika Toczyńska		
ADRES INWESTYCJI: ul. VI Poprzeczna 23, 04-620 Warszawa	NR RYS.	SKALA
	10	1:50
		A3
FORMAT		
Marzec 2023		



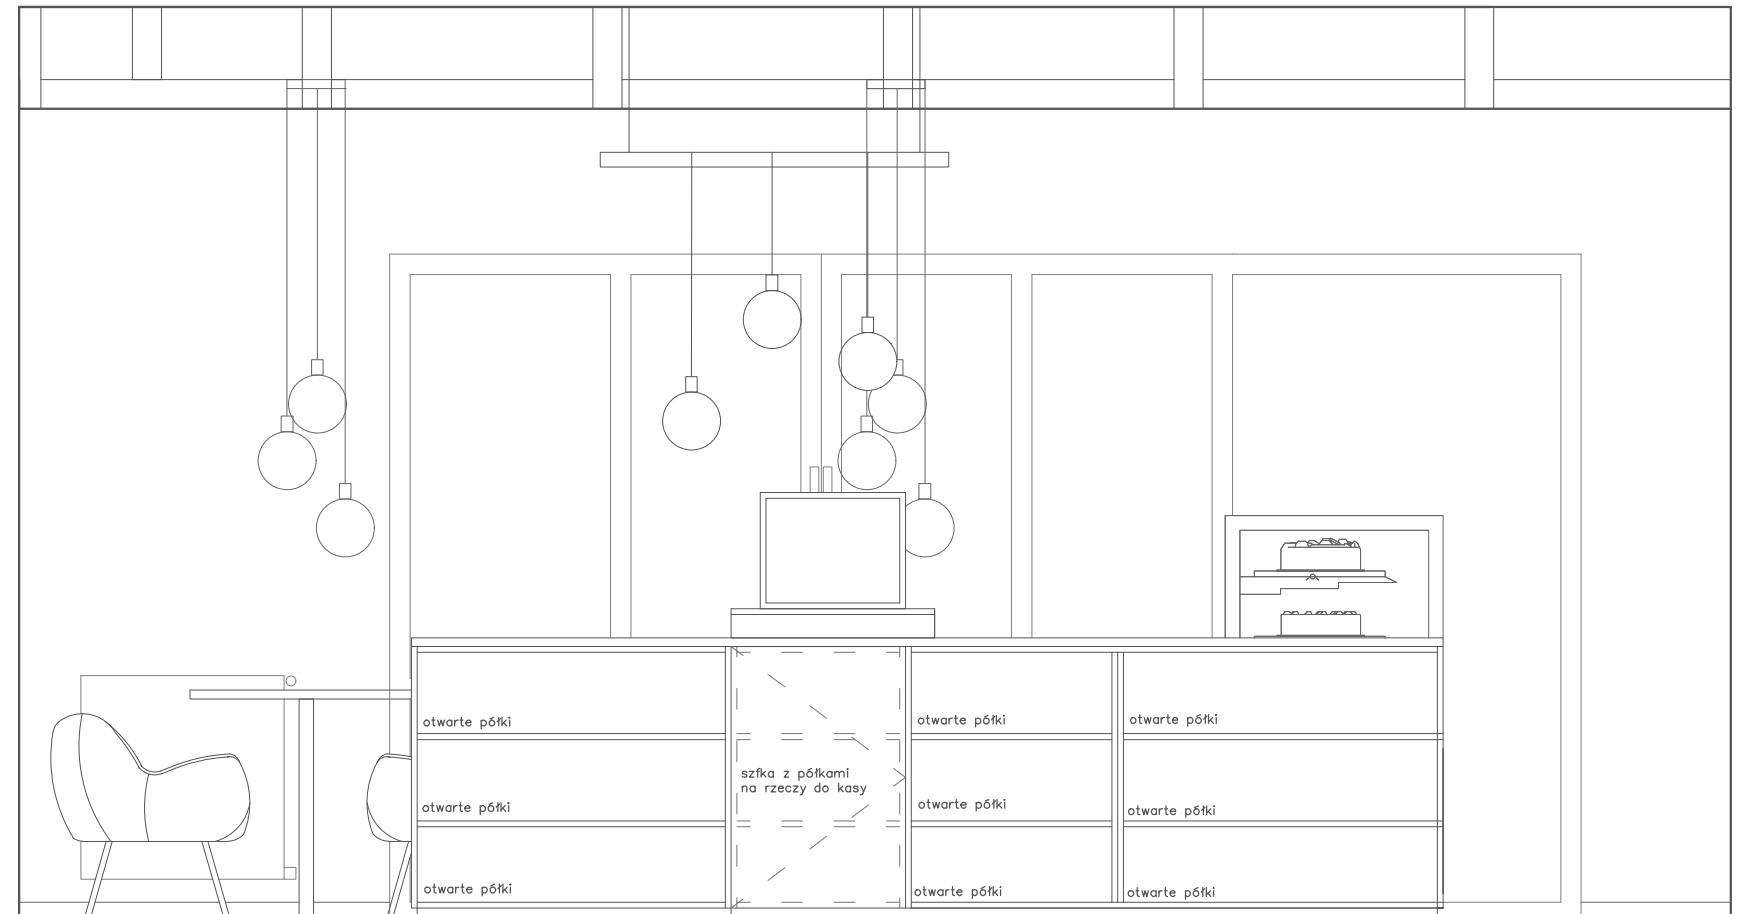


110 60 70 110 95
355 95


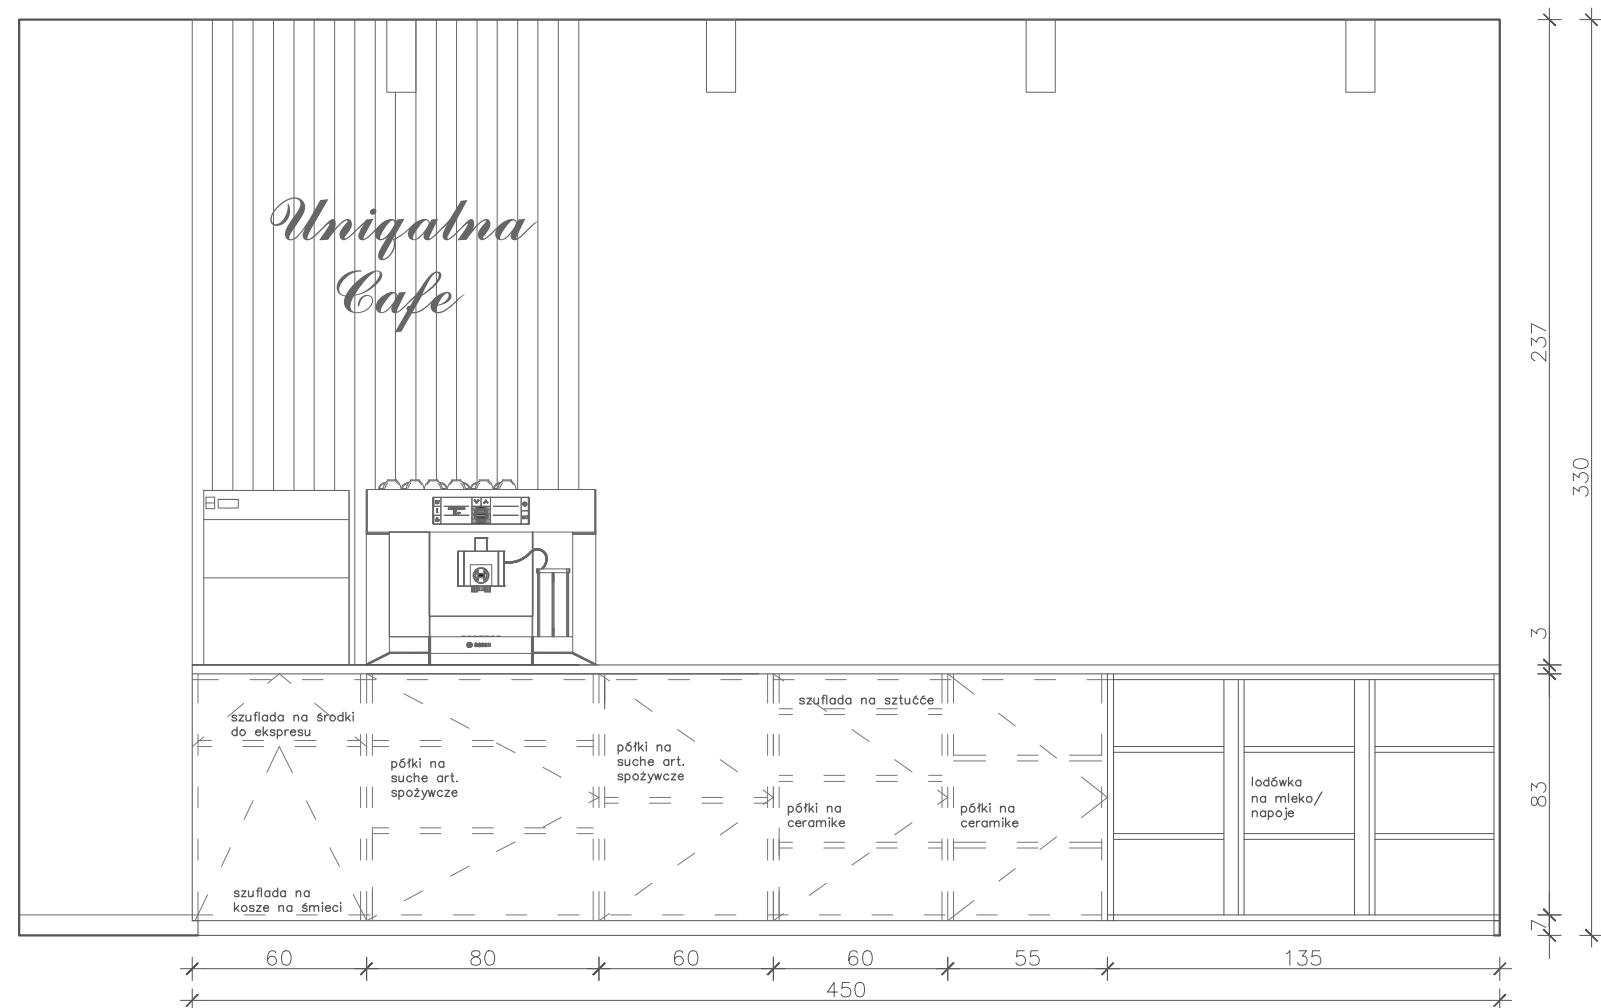


60 80 60 60 55 135
450

NAZWA RYSUNKU: Projekt wnętrza kawiarni otwartej sezonowo na ogródek zewnętrzny dla młodzieży	PODPIS:	
Dominika Toczyńska		
ADRES INWESTYCJI: ul. VI Poprzeczna 23, 04-620 Warszawa		
NR RYS.	SKALA	FORMAT
12	1:25	A3
Marzec 2023		

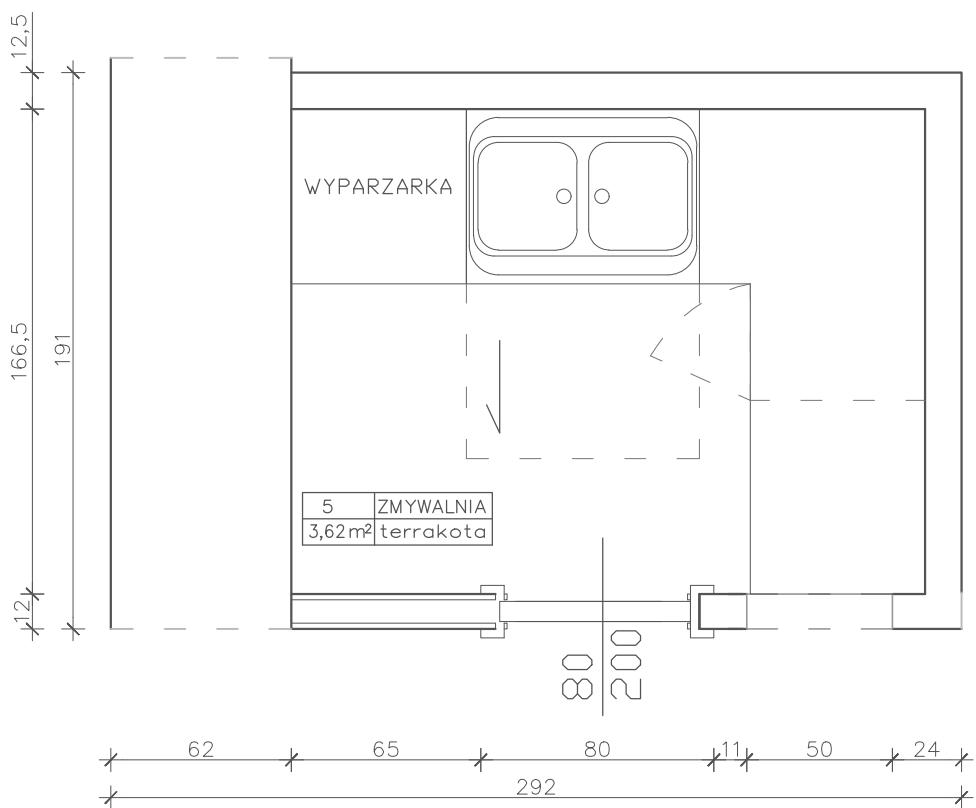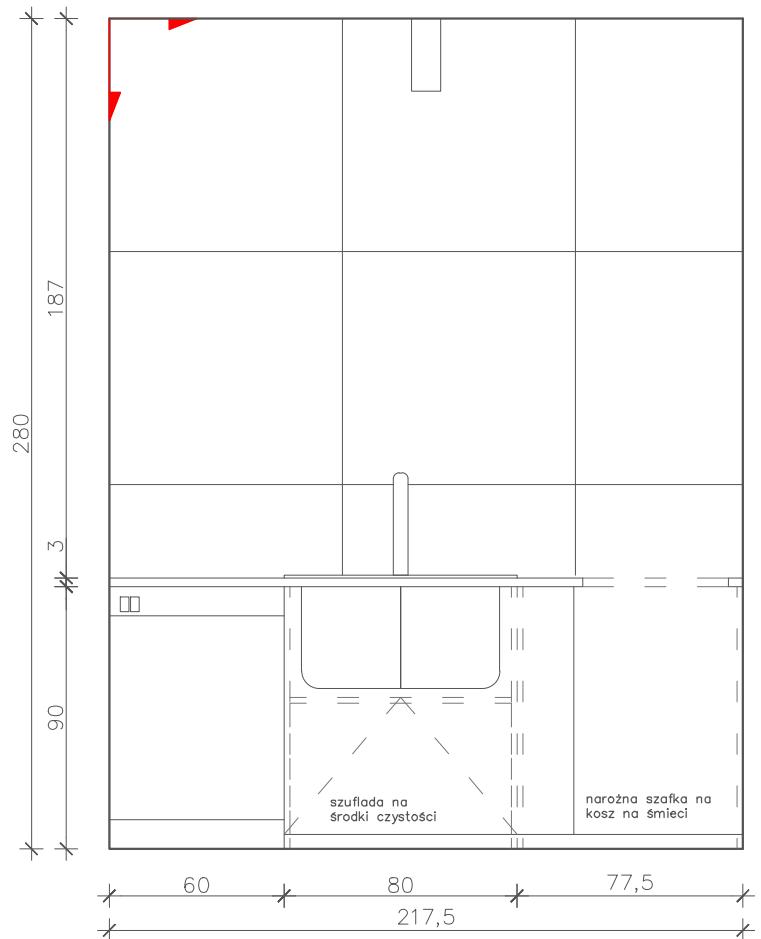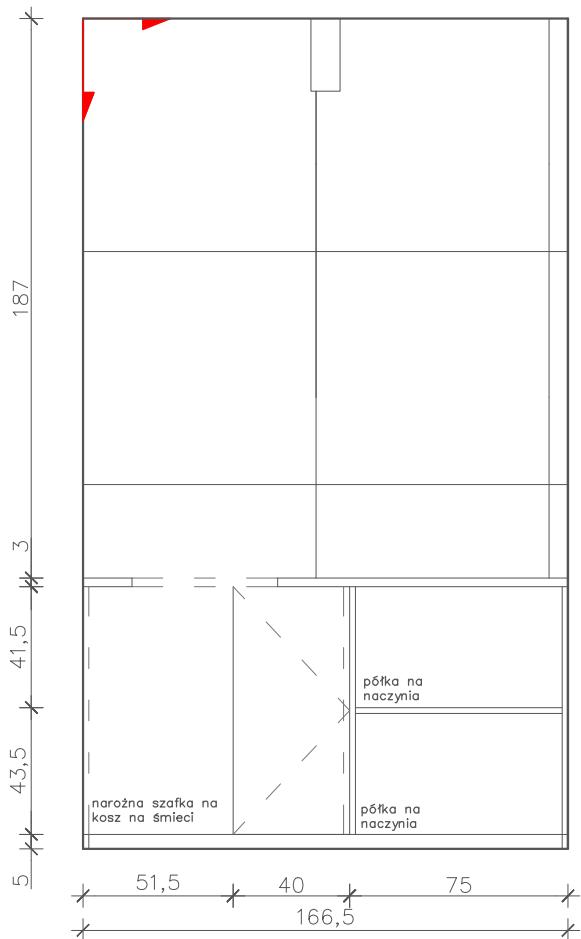

NAZWA RYSUNKU: Projekt wnętrza kawiarni otwartej sezonowo na ogródek zewnętrzny dla młodzieży SKŁADÓWANIE ZMYWALNI		
DPRACOWANIE: Dominika Toczyńska		
ADRES INWESTYCJI: ul. VI Poprzeczna 23, 04-620 Warszawa		
NR RYS.	SKALA	FORMAT
13	1:25	A4
Marzec 2023		

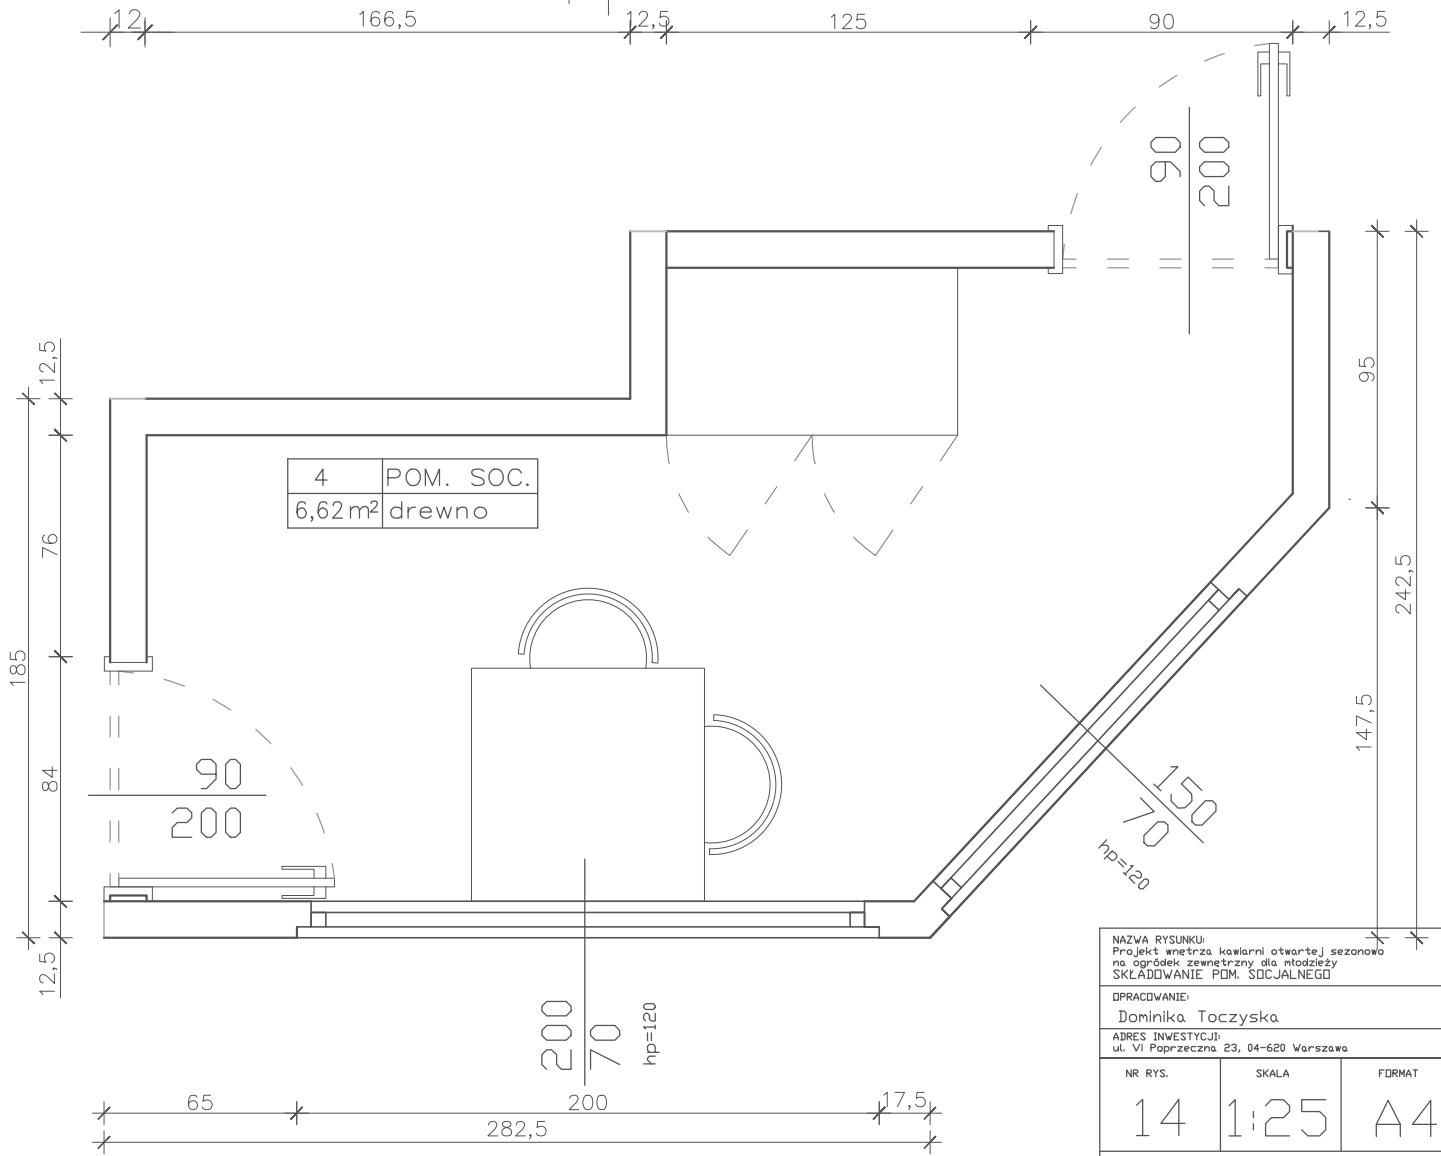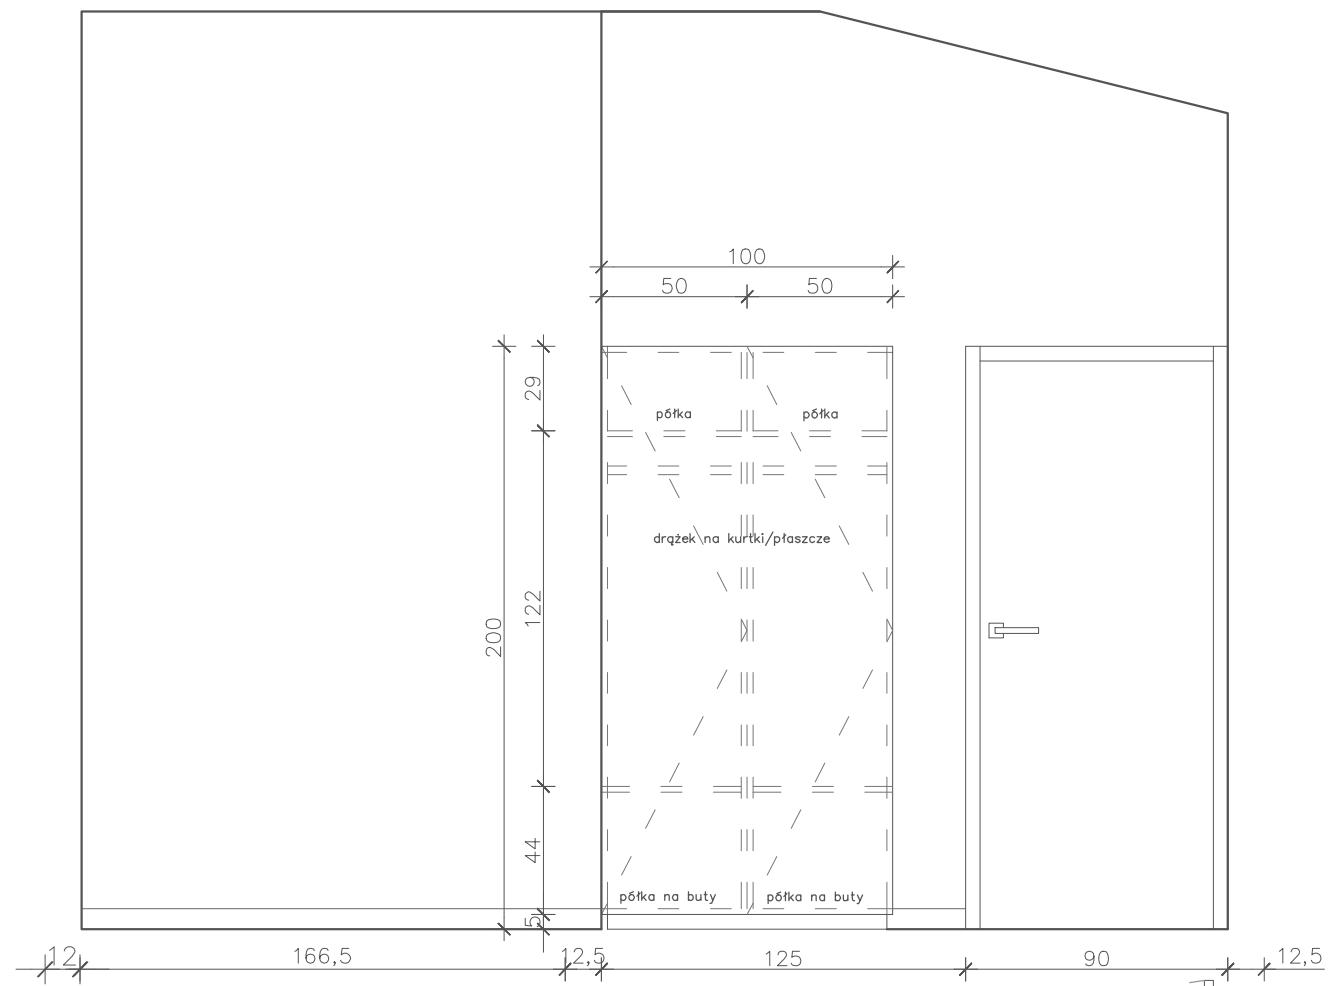



NAZWA RYSUNKU:
Projekt wnętrza kawiarni otwartej sezonowo
na ogródek zewnętrzny dla młodzieży
SKŁADÓWANIE PDM. SOCYJALNEGO

DOPRACOWANIE:
Dominika Toczyńska

ADRES INWESTYCJI:
ul. VI Poprzeczna 23, 04-620 Warszawa

NR RYS.	SKALA	FORMAT
14	1:25	A4




Marzec 2023

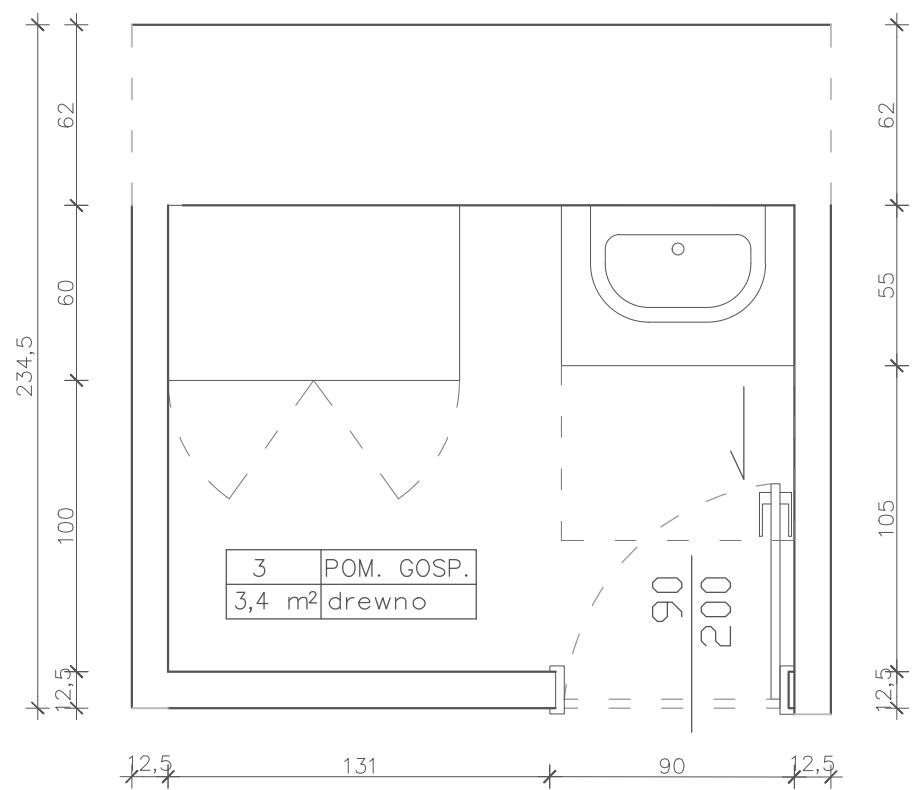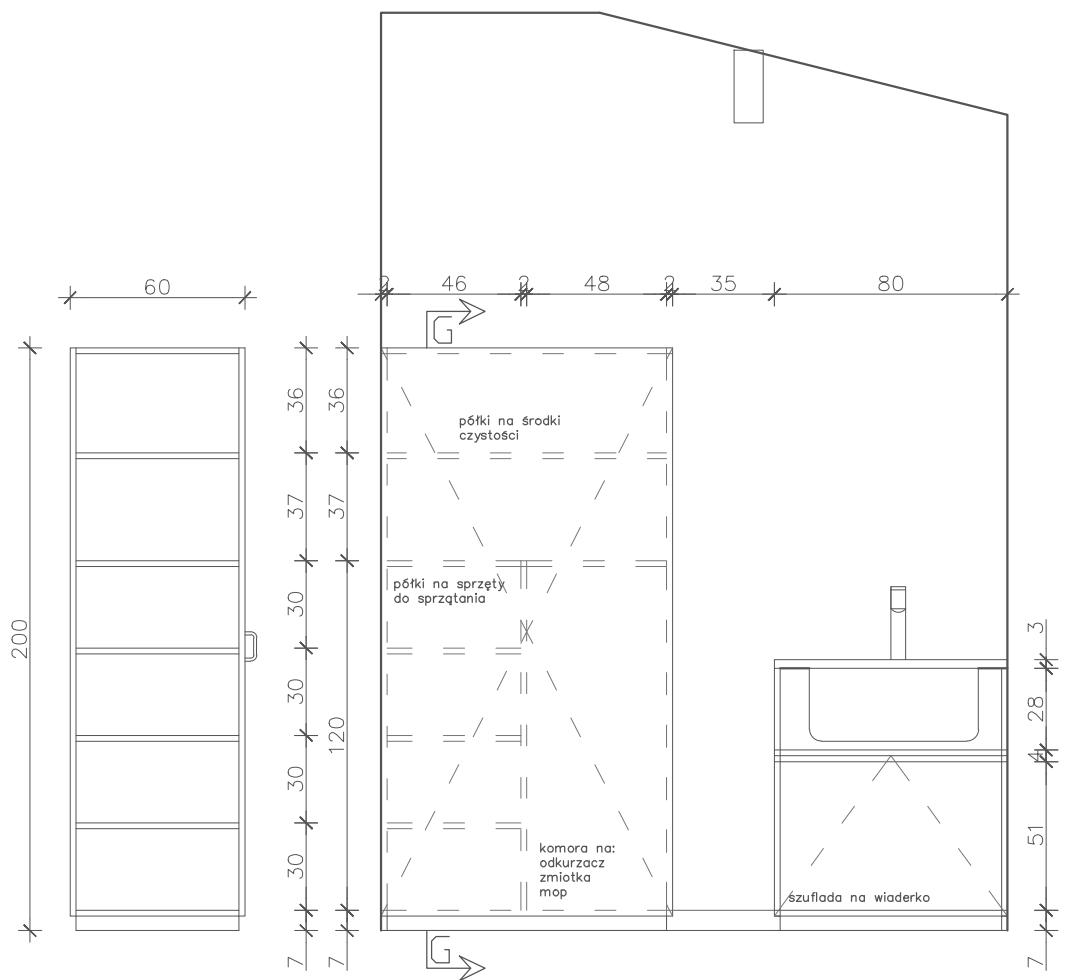

NAZWA RYSUNKU: Projekt wnętrza kawiarni otwartej sezonowo na ogródek zewnętrzny dla młodzieży SKŁADANIE PDM. GOSPODARCZEGO		
DPRACOWANIE: Dominika Toczyńska		
ADRES INWESTYCJI: ul. VI Poprzeczna 23, 04-620 Warszawa		
NR RYS.	SKALA	FORMAT
15	1:25	A4
Marzec 2023		


DETAL LAMELI

Lamela zwijająca się na bokach pergoli obraca się, dzięki czemu chroni one przed wieloma warunkami atmosferycznymi

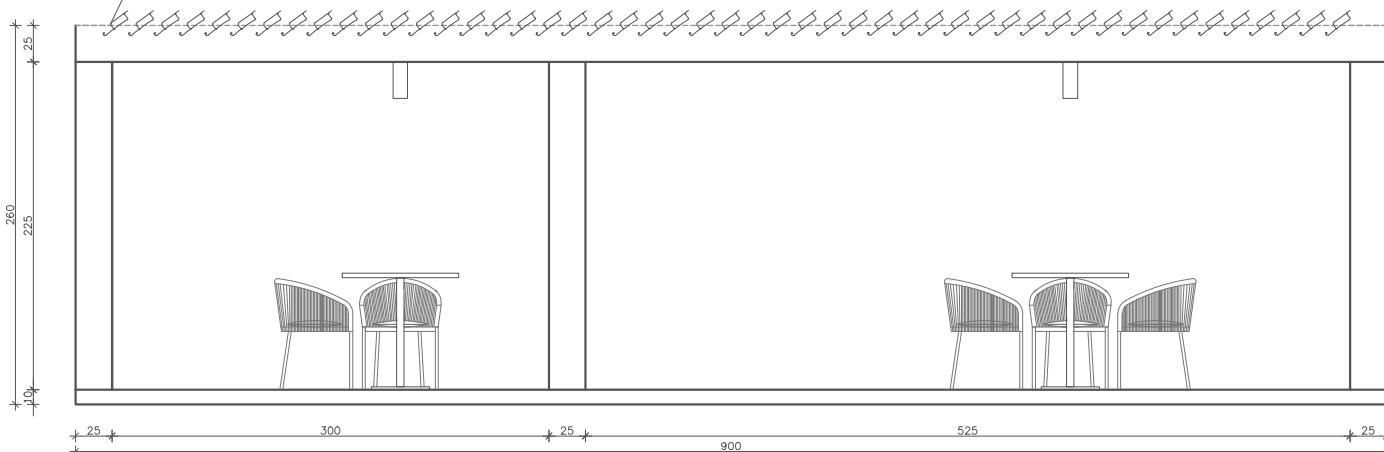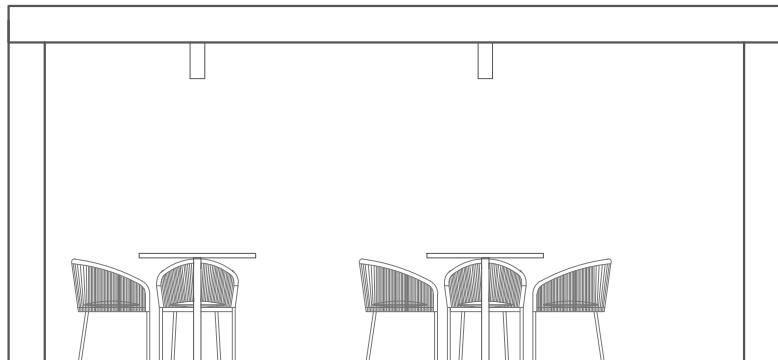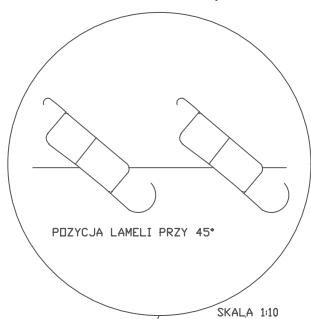



PRZEKRÓJ F-F

E

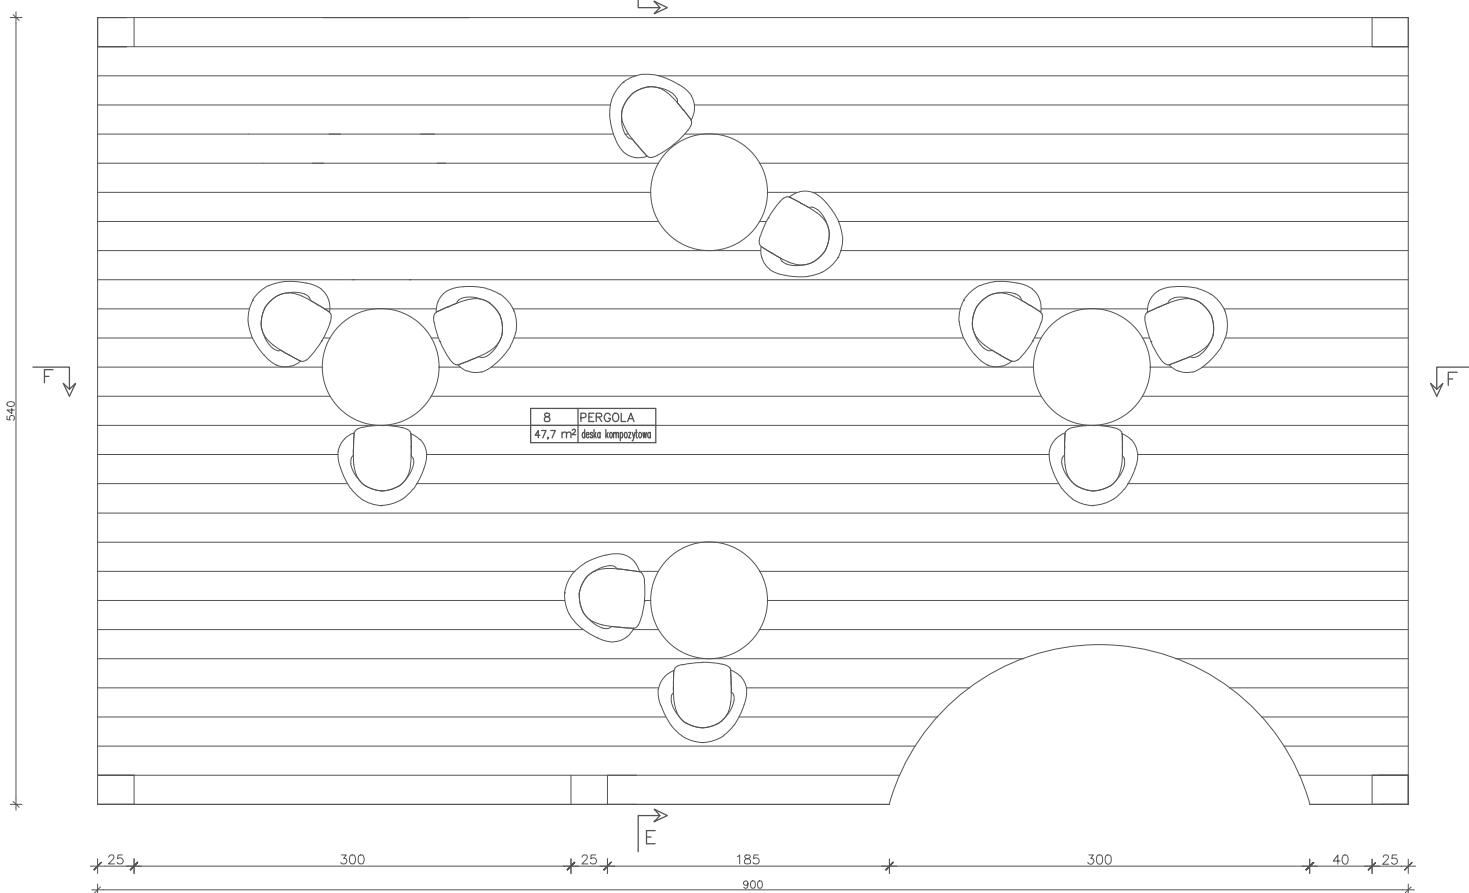

RZUT

NAZWA RYSUNKU: Projekt wnętrza kawiarni otwartej sezonowo na ogródek zewnętrzny dla młodzieży PERGOLA-PRZEKRÓJ E-E, F-F I DETAL LAMELI		
DOPRACOWANIE: Dominika Toczyńska		
ADRES INWESTYCJI: ul. VI Poprzeczna 23, 04-620 Warszawa		
NR RYS.	SKALA	FORMAT
16	1:50	A4
Marzec 2023		

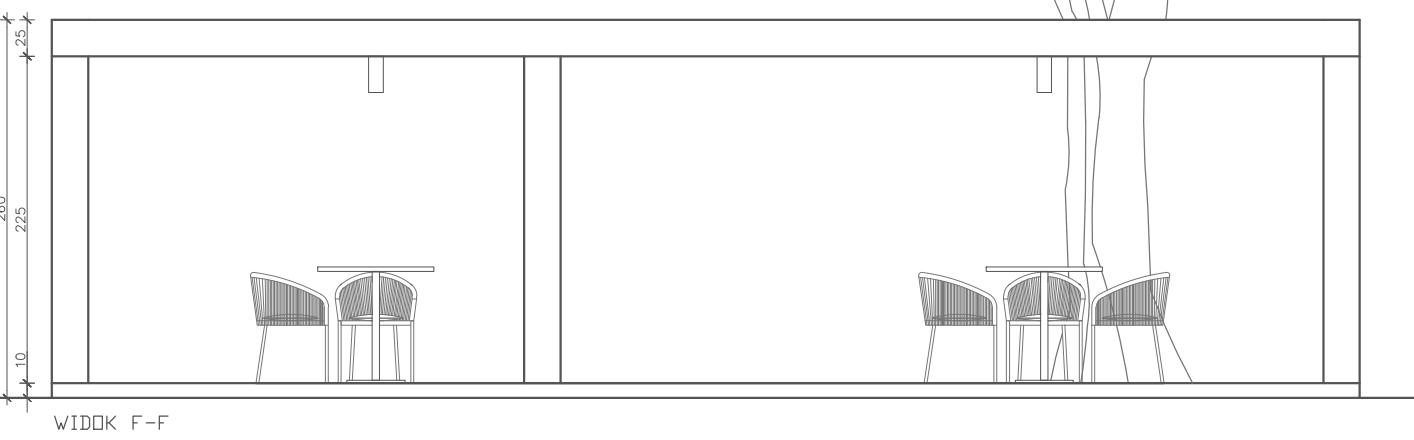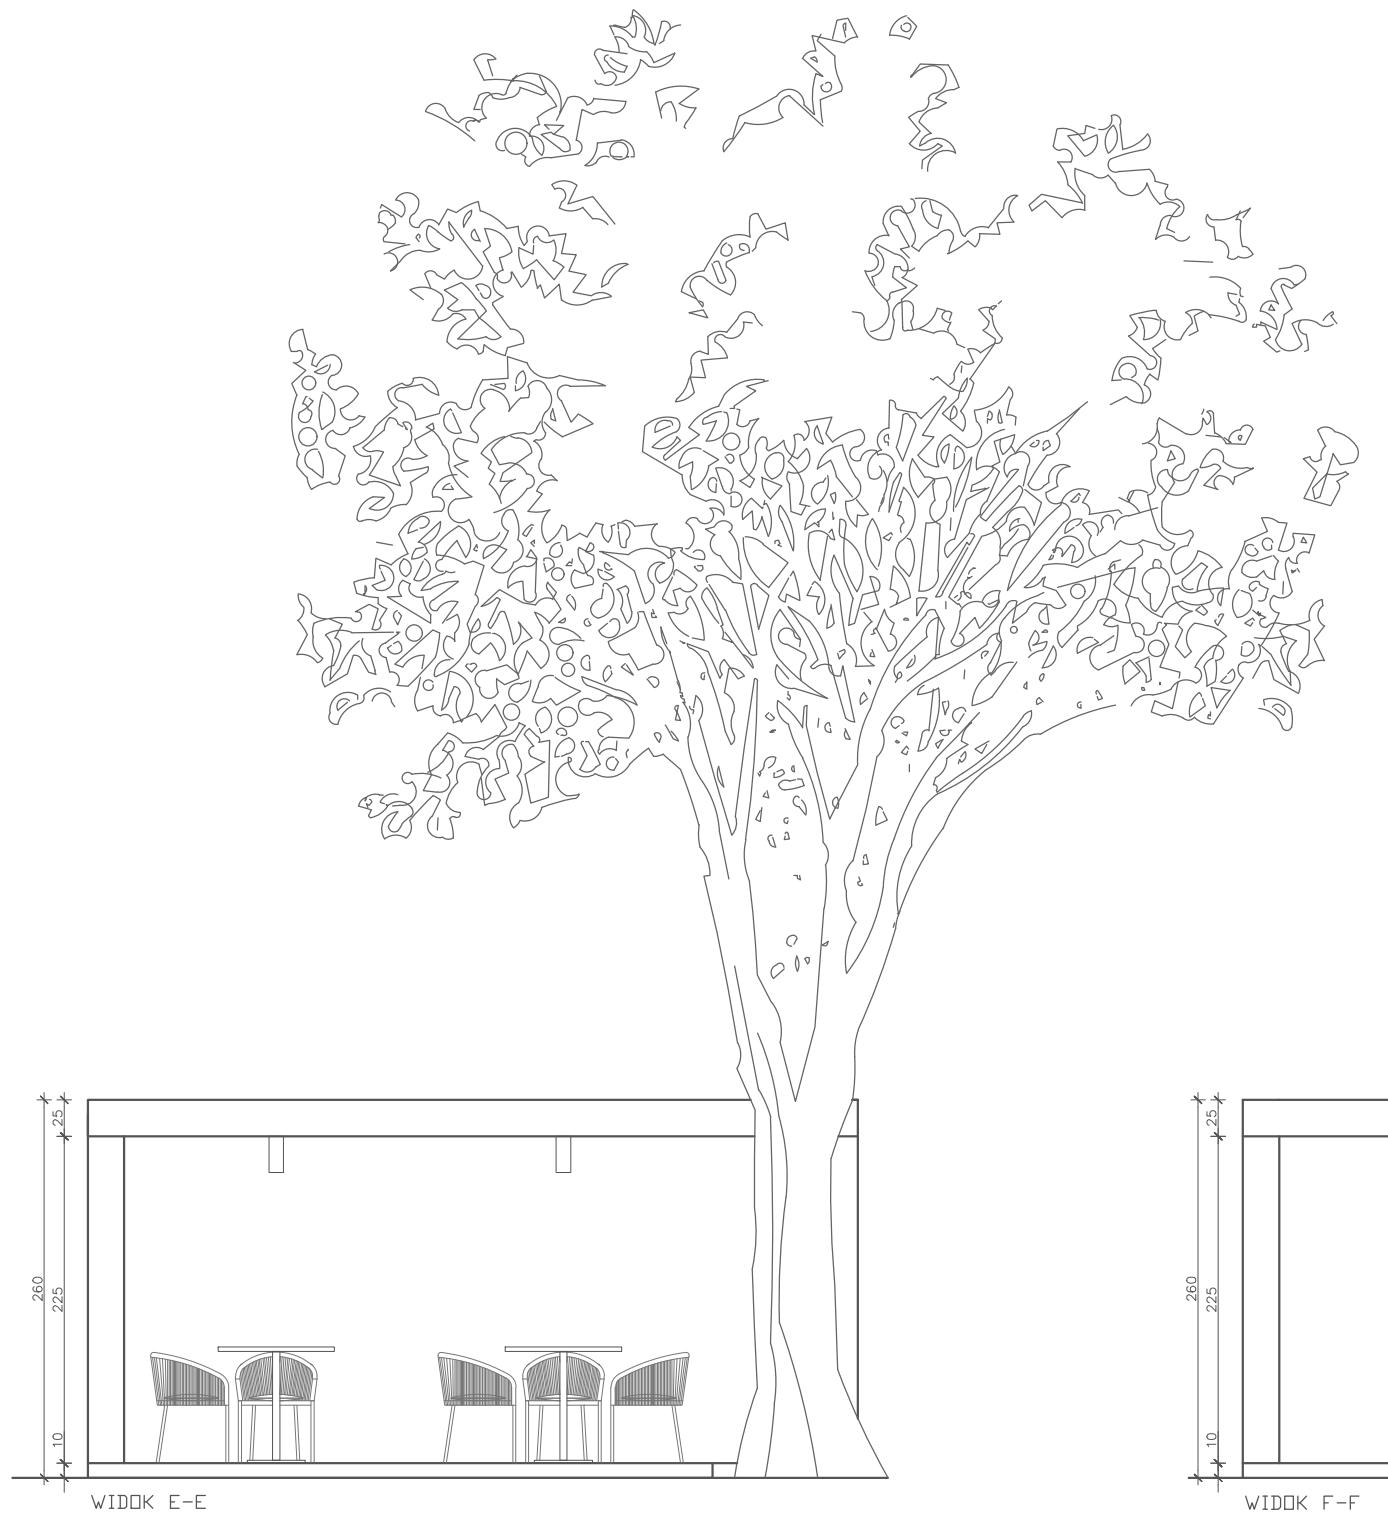


NAZWA RYSUNKU: Projekt wnętry kawiarni otwartej sezonowo na ogródek zewnętrzny dla młodzieży PERGOLA WIDOK E-E, F-F		
DOPRACOWANIE: Dominika Toczyńska		
ADRES INWESTYCJI: ul. VI Poprzeczna 23, 04-620 Warszawa		
NR RYS.	SKALA	FORMAT
17	1:50	A3
Marzec 2023		



NAZWA RYSUNKU: Projekt anekta kawiarni otwartej sezonowo na ogródek zewnętrzny dla młodzieży RZUT KOLORYSTYCZNY		
OFRACOWANIE: Dominika Toczyńska		
ADRES INWESTYCJI: ul. VI Poprzeczna 23, 04-620 Warszawa		
NR RYS.	SKALA	FORMAT
18	1:50	A3
Marzec 2023		




WIDOK KOLORYSTYCZNY A-A

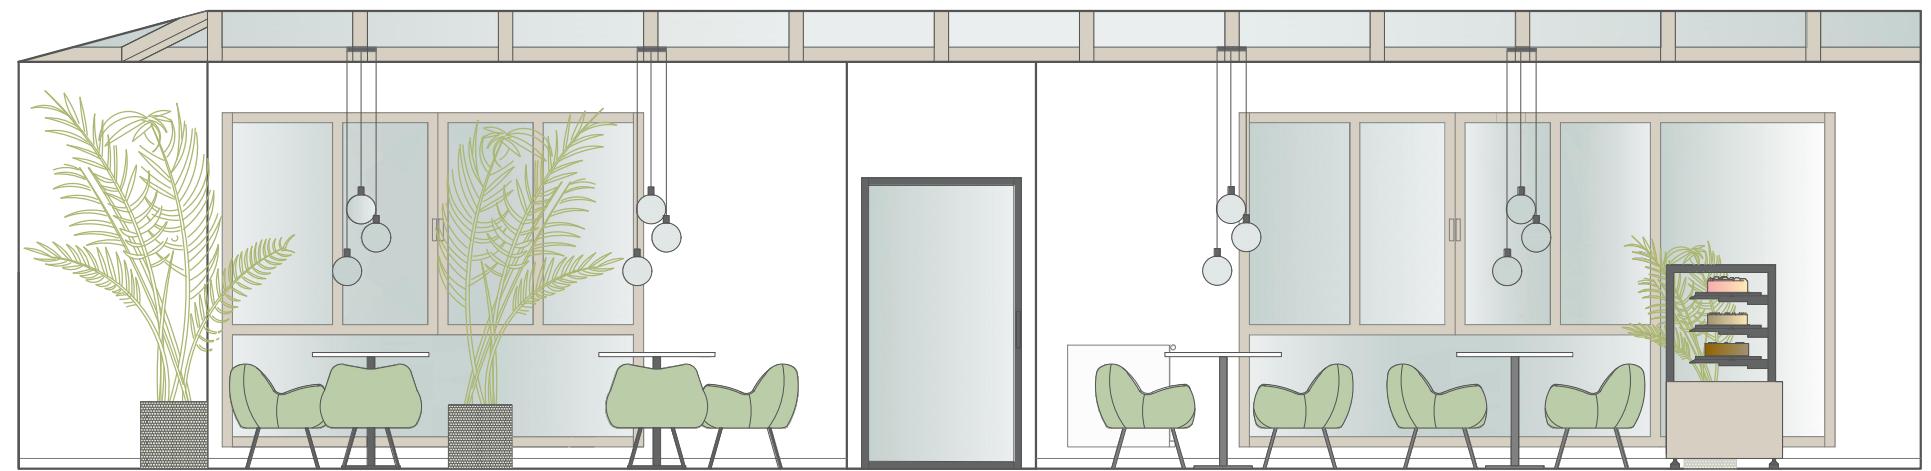

WIDOK KOLORYSTYCZNY B-B





WIDOK KOLORYSTYCZNY C-C

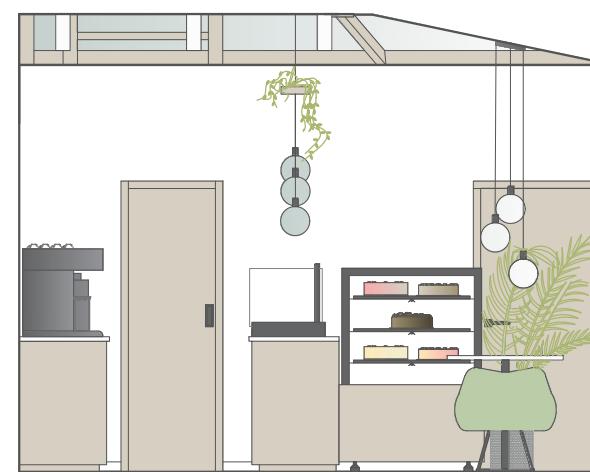

WIDOK KOLORYSTYCZNY D-D


NAZWA RYSUNKU: Projekt aneksu kawiarni otwartej sezonowo na ogródku zewnetrzny dla młodzieży		
WIDOKI KOLORYSTYCZNE A-A, B-B, C-C, D-D		
OPRACOWANIE: Dominika Toczyńska		
ADRES INWESTYCJI: ul. VI Poprzeczna 23, 04-620 Warszawa		
NR RYS.	SKALA	FORMAT
19	1:50	A3
Marzec 2023		

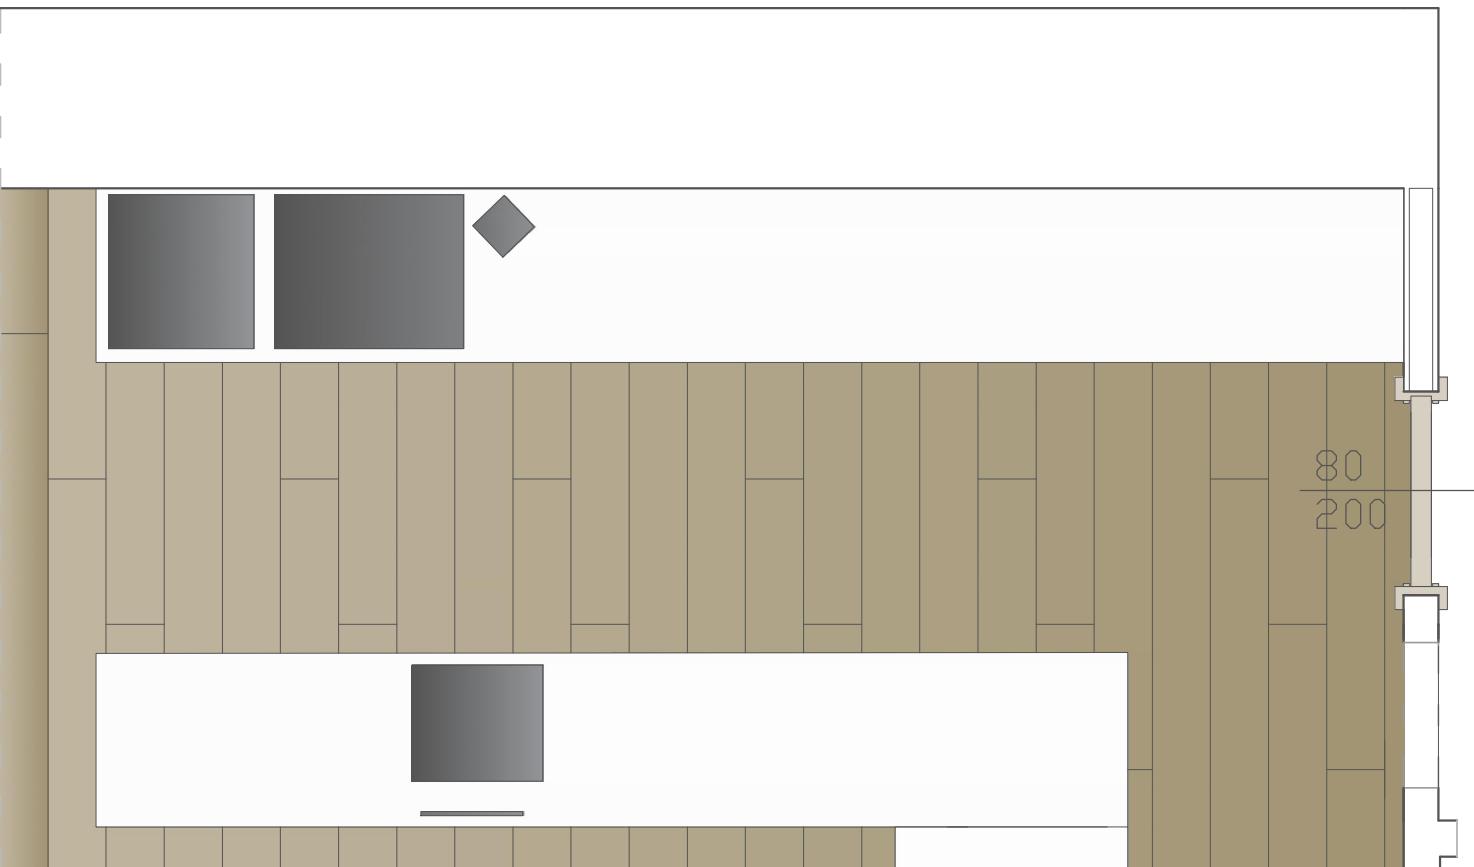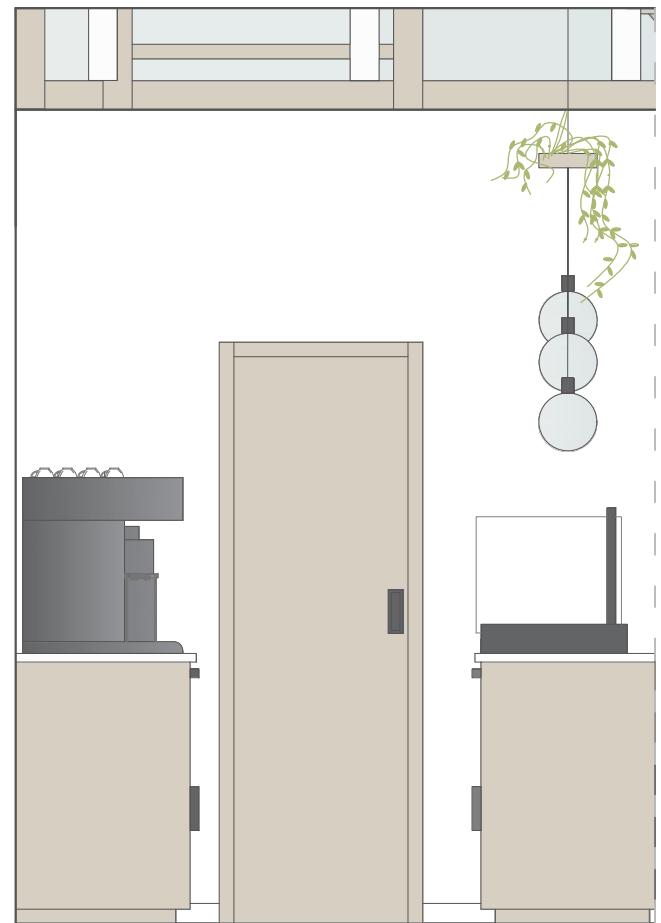

NAZWA RYSUNKU:
 Projekt wnętrza kawiarni otwartej sezonowo
 na ogródek zewnętrzny dla młodzieży
 WIDOKI KOLORYSTYCZNE BARU
 PRACODAWCA:
 Dominika Toczyńska
 ADRES INWESTYCJI:
 ul. VI Poprzeczna 23, 04-620 Warszawa
 NR RYS. SKALA FORMAT
 20 1:25 A3
 Marzec 2023




WIDOK KOLORYSTYCZNY E-E

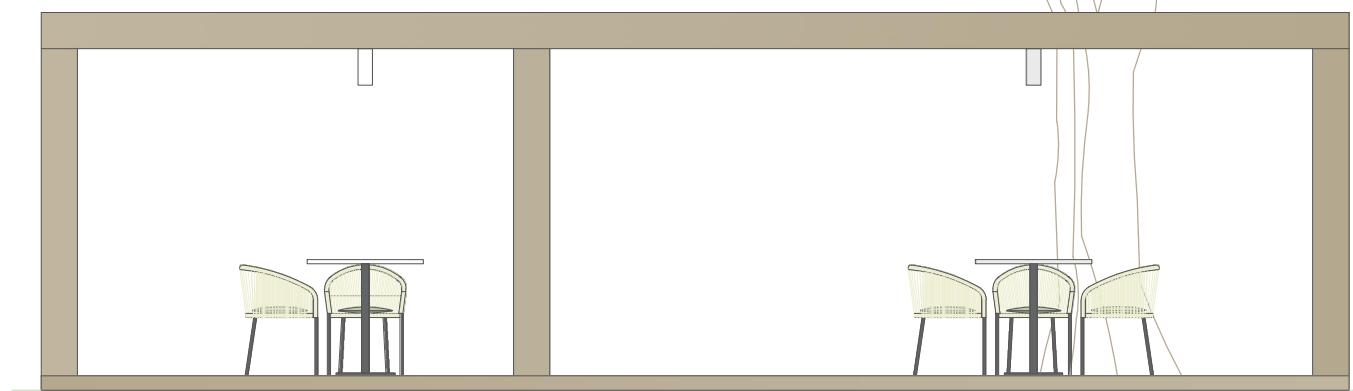

WIDOK KOLORYSTYCZNY F-F

NAZWA RYSUNKU: Projekt wnętrza kawiarni otwartej sezonowo na ogródek zewnętrzny dla młodzieży PERGOLA WIDOK KOLORYSTYCZNY E-E, F-F		
DOPRACOWANIE:		
Dominika Toczyńska		
ADRES INWESTYCJI:	ul. VI Poprzeczna 23, 04-620 Warszawa	
NR RYS.	SKALA	FORMAT
21	1:50	A3
Marzec 2023		

III. Specyfikacja wyposażenia

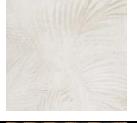1.	DĄB CIEPŁY BRĄZOWY CLASSIC CLM5789	
2.	LISTWA PRZYPODŁOGOWA BIAŁA Z POWŁOKĄ WODOODPORNA – MDF LAKIEROWANY BIAŁY RAL900C	
3.	TAPETA LIŚCIE PALMY KHORMA LIVIA GLA920	
4.	PANEL ŚCIENNY LAMELE W KOLORZE CIEPŁEGO DĘBU	
5.	FARBA WODOODPORA MAGNAT CERAMIC B5 W KOLORZE CZYSTA BIEL	
6.	BLANCO NATURAL 80X80 BIAŁY GRES MAT	
7.	FOTEL MODZELEWSKIEGO RM58 SOFT TAPICEROWANY	
8.	DREWNIANA ŁAWA DĘBOWA	
9.	STÓŁ DO KAWIARNI ASTRID Ø 700 mm, laminat, biały, czarny	
10.	WITRYNA CUKIERNICZA SONATA 0.9 MAWI	
11.	BLAT BIAŁY YRKE	

12.	FRONTY SZAFEK W KOLORZE JASNEGO DĘBU	
13.	DONICA OGRODOWA RATTAN	
14.	ZWISAJĄCA LAMPA BOCCI	
15.	SPOT SUFITOWY DESIGNERSKI TUBA EYE TONE GU10 ŚR. 8,9CM BIAŁY ZŁOTY	
16.	DESKA TARASOWA DĘBOWA CIEPŁY BRAZ	
17.	KRZESŁO OGRODOWE KAVE HOME YANET	